ओएनजीसी ONGC	**ENGINEERING SECTION – ENGINEERING & PROJECTS EXCELLENCE CENTRE**	**ADDENDUM**	**DATE**	23.04.2026
			PROJECT NAME:	BRRP
			PAGE	**1 OF 1**

Reference No: Bridge Refurbishment & Replacement Project of MH Asset (BRRP), Tender No.: ZW1PC26002

Sl.No.	Vol.No./ Spec. No.	Modification
1	Technical SCC	Revised Technical SCC is attached.
2	A-3 Proforma for Price Schedule	Revised A3 attached.
3	Suggested Vendor list	Latest SVL attached (Rev 12.3)
4	Electrical, Piping, Structure & Instrumentation drawings and Specification	Documents pertaining to Electrical, piping, Structure and Instrumentation section are added.

ANNEXURE - 1: TENTATIVE DETAILED ENGINEERING DELIVERABLE

ANALYSIS REQUIREMENT OF BRIDGE, DECK						Design Basis & Construction Methodology	Reports	AFC Drawings	Fabrication Drawing	As-Built Drawings	Tender Drawing (Strenthening only for reference)
Sr. No	**BRIDGE / PLATFORM**	**Surveys**	**New / Replace / Strenthening**	**Analysis Type**	**Remarks**						
1	ICW-ICG UD	1. Pre-Engineering Survey reports for all bridges, platforms. 2. NDT survey reports for all platforms. 3. Laser scanning Survey reports, if any, performed by contractor. 4. Pre-Construction Survey reports for all bridges, platforms. 5. Post-Construction Survey reports for all bridges, platforms.	Strenthening	Global Bridge	Bridge	1. Design basis to be prepared as per ONGC design criteria attacthed in the tender for approval 2. Construction / Installation Methodology for each bridge, landing strenthening shall be submitted seperately for approval	Approval	Approval	Records	Records	Refer Annexure -2 with TQ reply.
2	ICW-ICG LD		New	Global Bridge, Lift, transportation	Bridge		Approval	Approval	Records	Records	
3	ICG-ICP UD		Strenthening	Global Bridge	Bridge		Approval	Approval	Records	Records	
4	ICG-ICP LD		New	Global Bridge, Lift, transportation	Bridge		Approval	Approval	Records	Records	
5	BHS-SLQ		Replacement	Global Bridge, Lift, transportation, Demolition & Removal	Bridge		Approval	Approval	Records	Records	
6	SLQ-WIS		Strenthening	Global Bridge	Bridge		Approval	Approval	Records	Records	
7	NQO-NQD		Strenthening	Global Bridge	Bridge		Approval	Approval	Records	Records	
8	WIN-NC		Strenthening	Global Bridge	Bridge		Approval	Approval	Records	Records	
9	SCA-SC1		Strenthening	Global Bridge	Bridge		Approval	Approval	Records	Records	
10	SCA-SCF		Strenthening	Global Bridge	Bridge		Approval	Approval	Records	Records	
11	ICP Platform		Strenthening	Global Deck Inplace	Landing and Global Deck		Approval	Approval	Records	Records	
12	ICG Platform		Strenthening	Global Deck Inplace	Landing and Global Deck		Approval	Approval	Records	Records	
13	ICW Platform		Strenthening	Global Deck Inplace	Landing and Global Deck		Approval	Approval	Records	Records	
14	BHS Platform		Strenthening	Global Deck Inplace	Landing and Global Deck		Approval	Approval	Records	Records	
15	SLQ Platform		Strenthening	Global Deck Inplace	Landing and Global Deck		Approval	Approval	Records	Records	
16	WIS Platform		Strenthening	Deck Local Inplace	Landing		Approval	Approval	Records	Records	
17	NOQ Platform		Strenthening	Deck Local Inplace	Landing		Approval	Approval	Records	Records	
18	NQD Platform		Strenthening	Deck Local Inplace	Landing		Approval	Approval	Records	Records	
19	WIN Platform		Strenthening	Deck Local Inplace	Landing		Approval	Approval	Records	Records	
20	NC Platform		Strenthening	Deck Local Inplace	Landing		Approval	Approval	Records	Records	
21	SC1 Platform		Strenthening	Deck Local Inplace	Landing		Approval	Approval	Records	Records	
22	SCA platform		Strenthening	Deck Local Inplace	Landing		Approval	Approval	Records	Records	
23	SCF platform		Strenthening	Deck Local Inplace	Landing		Approval	Approval	Records	Records	

Note: The provided list is not complete. It is contractors responsibility to develop and provide all documentation, drawings, technical notes, sketches, etc required to complete the works.

Sr. No	DRAWING NUMBER	Rev No	DESCRIPTION	BRIDGE / PLATFORM	No. OF SHEETS
1	B774-000-83-43-0001	0	General Notes	Common	2
2	B774-001-83-43-0001	0	ICW-ICG Upper Deck drawing – Strengthening and modifications.	ICW-ICG Upper Deck	
3	B774-002-83-43-0001	A	ICP-ICG Upper Deck drawing – Strengthening and modifications.	ICP-ICG Upper Deck	
4	B774-002-83-43-0002	A	ICP-ICG Upper Deck drawing – Strengthening and modifications.	ICP-ICG Upper Deck	
5	B774-003-83-43-0001	0	NQO-NQD Upper Deck drawing – Strengthening and modifications.	WIS-SLQ Lower deck Bridge	
6	B774-003-83-43-0002	0	WIS Landing Area - Modification	WIS Platform	
7	B774-004-83-43-0001	0	WIS-SLQ Upper Deck drawing – Strengthening and modifications.	NQO-NQD Bridge	
8	B774-004-83-43-0002	A	NQO Landing Area - Modification	NQO Platform	
9	B774-004-83-43-0003	A	NQO Landing Area - Modification	NQO Platform	
10	B774-004-83-43-0004	A	NQD Landing Area - Modification	NQD Platform	
11	B774-004-83-43-0005	A	NQD Landing Area - Modification	NQD Platform	
12	B774-005-83-43-0001	0	WIN-NC Bridge drawing – Strengthening and modifications.	WIN-NC Bridge	
13	B774-005-83-43-0002	0	WIN Landing Area - Modification	WIN Platform	
14	B774-005-83-43-0003	0	WIN Landing Area - Modification	WIN Platform	
15	B774-005-83-43-0004	0	NC Landing Area -	NC Platform	

Copyrights EIL – All rights reserved

			Modification		
16	B774-007-83-43-0001	0	SC1-SCA Bridge drawing – Strengthening and modifications.	SC1-SCA Bridge	
17	B774-007-83-43-0002	A	SC1 Landing Area - Modification	SC1 Platform	
18	B774-007-83-43-0003	A	SCA Landing Area - Modification	SCA Platform	
19	B774-008-83-43-0001	0	SCA-SCF Bridge drawing – Strengthening and modifications.	SC1-SCA Bridge	
20	B774-008-83-43-0003	0	SCF Flare boom, Tripod Modification	SCF Platform	
21	B774-101-83-43-0001	0	ICW-ICG Lower Deck bridge drawings	ICW-ICG Lower Deck	
22	B774-101-83-43-0002	A	ICW Landing Area - Modification	ICW Platform	
23	B774-101-83-43-0003	A	ICW Landing Area - New Extensions	ICW Platform	
24	B774-101-83-43-0004	A	ICG Landing Area - Modification	ICG Platform	
25	B774-102-83-43-0001	A	ICP-ICG Lower Deck bridge drawings	ICP-ICG Lower Deck	2
26	B774-102-83-43-0002	A	ICP Landing Area - Modification	ICP Platform	
27	B774-102-83-43-0003	A	ICP Landing Area - New Extensions	ICP Platform	
28	B774-102-83-43-0004	A	ICG Landing Area - Modification	ICG Platform	
29	B774-103-83-43-0001	0	BHS-SLQ Lower Deck bridge drawings	BHS-SLQ Lower Deck (New)	
30	B774-103-83-43-0002	A	BHS Landing Area - Modification	BHS Platform	
31	B774-103-83-43-0003	A	BHS Landing Area - New Extensions	BHS Platform	
32	B774-103-83-43-0004	0	SLQ Landing Area - Modification	SLQ Platform	
33	B774-103-83-43-0005	0	SLQ Landing Area -	SLQ Platform	

Copyrights EIL – All rights reserved

			New Extensions		
34	B774-103-83-43-0006	0	BHS – SLQ Bridge Demolition Drawings	BHS-SLQ Lower Deck (Existing)	

Copyrights EIL – All rights reserved

यह ड्राइंग आरेख एवं इसमें निहित डिज़ाइन इंजीनियर्स इंडिया लिमिटेड की संपत्ति है। ये मात्र उधार दिए गए हैं और उधारकर्ता ने यह स्पष्ट समझौता किया है कि ये न तो उन्हें दूसरे, गुप्तित किया जाएगा, न प्रकाश की जाएगी, न उधार दिए जाएंगे, न प्रतिलिपि किए जाएंगे और न ही संलिप्त और किसी प्रयोग के अलावा इसका कोई अन्य प्रयोग करेंगे अन्य प्रयोग हेतु और यह प्रयोग उधार देने वाले द्वारा उधारकर्ता को लिखित रूप में दी गई सहमति से होगा।
The drawing, design and details given on this format are the property of ENGINEERS INDIA LIMITED. They are merely loaned on the borrower's express agreement that they will not be reproduced, copied, exhibited or used, except in the limited way permitted by a written consent given by the lender to the borrower for the intended use.

B774-000-83-43-0001

S.NO.	GENERAL
1.	THE NOTES CONTAINED IN THIS DRAWING PERTAIN TO ALL DRAWINGS LISTED UNDER DECK DRAWINGS AND MODULE DRAWINGS IN DRAWING INDEX. IF A CONFLICT OCCURS BETWEEN ANY OF THESE NOTES AND THE DRAWINGS , THE NOTES GIVEN IN INDIVIDUAL DRAWINGS SHALL GOVERN.
2.	ALL MAIN STRUCTURAL MEMBERS INDICATED ON THESE DRAWINGS HAVE BEEN DETERMINED FROM DESIGN WORK PERFORMED IN CONFORMANCE WITH THE FOLLOWING: a) STRUCTURAL DESIGN CRITERIA DESCRIBED IN BID PACKAGE. b) LATEST EDITION OF API RECOMMENDED PRACTICE 2A WSD FOR PLANNING, DESIGNING AND CONSTRUCTING FIXED OFFSHORE PLATFORMS. c) LATEST EDITION OF AISC SPECIFICATION FOR THE DESIGN, FABRICATION AND ERECTION OF STRL. STEEL FOR MODULES. d) CRITERIA FOR EARTHQUAKE DESIGN AS PER IS:1893/API RP 2A/API RP 2EQ e) API RECOMMENDED PRACTICE 2L FOR PLANNING, DESIGNING AND CONSTRUCTING HELIPORTS FOR FIXED OFFSHORE PLATFORMS AND ICAO GUIDELINES. f) OTHER SPECIFIC REQUIREMENTS OF THE BID PACKAGE.
3.	ALL DIMENSIONS SHOWN ON THESE DRAWINGS ARE IN MILLIMETRES AND ALL LEVELS SHOWN ARE IN METRES W.R.T CHART DATUM.
4.	FOR TUBULAR SECTIONS, UB SECTIONS, INDIAN ROLLED SECTIONS AND PLATES, SIZES ARE SHOWN IN MM AND FOR W SHAPE AND AMERICAN STANDARD CHANNELS, THE SIZES ARE SHOWN IN INCHES.
5.	THE FOLLOWING ABBREVIATIONS HAVE BEEN USED IN THESE DRAWINGS: C/C : CENTER TO CENTER COND : CONDUCTOR CHQD. : CHEQUERED ℄ / CL : CENTER LINE COL : COLUMN DET : DETAIL DIA : DIAMETER DIAPH : DIAPHRAGM DK : DECK DWG/DRG : DRAWING EA : EACH EL : ELEVATION EQ : EQUAL EXT : EXTERIOR EXTN : EXTENSIONS FL : FLANGE FS : FAR SIDE GALV : GALVANISED GRAT : GRATING GS : GENERAL SPECIFICATIONS HD : HEAD HR : HANDRAIL HXG : HEXAGONAL ICAO : INTERNATIONAL CIVIL AVIATION ORGANIZATION INT : INTERNAL ISMB : BEAM SECTION AS PER IS ISMC : CHANNEL SECTION AS PER IS JKT : JACKET KSI : KIPS PER SQ. INCH L : ANGLE MIN : MINIMUM MECH : MECHANICAL MM : MILLIMETRES Mpa : MEGA PASCAL NB : NOMINAL BORE NOS. : NUMBERS NS : NEAR SIDE NTS : NOT TO SCALE ø : OUTER DIAMETER O/O : OUT TO OUT OPP : OPPOSITE PC : PIECE ℗ : PLATE PL : PLATE RAD : RADIUS REF : REFER REQD : REQUIRED SCH : SCHEDULE SEC : SECTION SHT/SH : SHEET SHW : SHOWN SPEC : SPECIFICATION SPCS : SPACES STIFF : STIFFENER STRL : STRUCTURAL STD : STANDARD THK/TH : THICK T.O.G. : TOP OF GRATING T.O.P. : TOP OF PLATE T.O.S. : TOP OF STEEL TYP : TYPICAL UB : UNIVERSAL BEAMS UNO : UNLESS NOTED OTHERWISE W : WIDE FLANGE W.P. : WORK POINT WSD : WORKING STRESS DESIGN

S.NO.	MATERIAL
1.	ALL MATERIALS INCLUDING STEEL, CEMENT AND TIMBER SHALL BE IN ACCORDANCE WITH MATERIAL SPEC. NO. 6-60-0011. i.e.STANDARD SPECIFICATION FOR STRUCTURAL MATERIALS
2.	HELIDECK PLATING SHALL BE AS PER SPECIFICATION 6-60-0011. i.e.STANDARD SPECIFICATION FOR STRUCTURAL MATERIALS
3.	EXCEPT WHERE SPECIFICALLY MENTIONED OTHERWISE IN THE DRAWINGS, THE FOLLOWING MARKINGS HAVE BEEN USED TO IDENTIFY THE GRADE OF STEEL MATERIAL AS PER MATERIAL SPEC. NO. 6-60-0011 i.e.STANDARD SPECIFICATION FOR STRUCTURAL MATERIALS I. FOR TUBULAR AND PLATES: a) TUBULARS USED IN JOINT CANS (25MM TH. AND ABOVE) FOR DECK LEGS AND CRANE PEDESTAL SHALL CONFIRM TO API SPEC. 2H (MIN. Fy =345 Mpa) OR EQUIVALENT (INTERMEDIATE STRENGTH STEEL WITH THROUGH THICKNESS PROPERTY) ▨ b) TUBULAR UPTO 406 mm DIA AND HANDRAIL SHALL BE SEAMLESS AS PER API SPEC 5L Grade B (MIN. Fy =240 Mpa.) OR EQUIVALENT. ☐ c) TUBULARS 457 mm DIA AND ABOVE TO BE USED IN IN DECK LEGS/ BRACES INCLUDING CRANE PEDESTAL AND JOINT CANS LESS THAN 25MM THICK SHALL BE ROLLED FROM PLATES AS PER API SPEC 2H Grade 50 (MIN. Fy =345 Mpa.) OR EQUIVALENT. ☐ II. FOR BEAMS: a) WIDE FLANGE BEAMS OF SIZE W 12 AND ABOVE SHALL CONFORM TO ASTM A 572 Grade 50 OR EQUIVALENT. b) WIDE FLANGE BEAMS OF SIZE LESS THEN W 12 SHALL CONFIRM TO ASTM A36 OR EQUIVALENT. c) ALL INDIAN SECTIONS SHALL BE OF MATERIAL CONFORMING TO IS:2062 Grade B.
4.	MATERIAL GRADE FOR ALL BEAM EXTENSION PLATES, WEB STIFFENERS BOX PLATES SHALL BE OF THE SAME GRADE WITH MATCHING PROPERTIES AS THE PARENT MATERIAL TO WHICH THEY ARE CONNECTED.
5.	ALL HANDRAILS & SOCKETS SHALL BE AS PER SPEC. NO. 6-60-0011 AND STRUCTURAL DESIGN BASIS.
6.	ALL GRATING AND STAIR TREADS SHALL BE GALVANISED 30 MM SERRATED BAR GRATING AND DETAILS AS PER SPEC. NO. 6-60-0011 i.e.STANDARD SPECIFICATION FOR STRUCTURAL MATERIALS
7.	ALL BOLTS SHALL CONFORM TO ASTM A193 Grade B7 OR EQUIVALENT AND NUTS SHALL CONFORM TO ASTM A194 Grade 2H AND SHALL BE HOT DIPPED GALVANISED.

S.NO.	FABRICATION AND WELDING
1.	ALL FABRICATION SHALL CONFORM TO THE FABRICATION SPEC NO. 6-60-0013 i.e.STANDARD SPECIFICATION FOR FABRICATION AND ASSEMBLY OF OFFSHORE STRUCTURES/COMPONENTS.
2.	ONLY FIGURED DIMENSIONS SHALL BE FOLLOWED. DIMENSIONS NOT SHOWN SHALL BE COMPUTED BUT NOT SCALED FROM THE DRAWINGS.
3.	WELDING AND WELD INSPECTION SHALL BE DONE IN ACCORDANCE WITH SPECIFICATION AND PROCEDURE.
4.	ALL MEMBERS SHALL INTERSECT AT A COMMON CENTER LINE WORK POINT (W.P.) AT ANY GIVEN JOINT UNLESS SHOWN OTHERWISE.
5.	ALL DECK BEAMS SHALL BE FLUSH AT TOP OF STEEL (T.O.S.) ELEVATION UNLESS OTHERWISE NOTED.
6.	DECK BEAM SPLICES IF USED, SHALL BE STAGGERED SO THAT THE JOINTS IN ANY TWO CONSECUTIVE BEAMS DO NOT OCCUR IN THE SAME LINE.
7.	UNLESS NOTED OTHERWISE THE FOLLOWING CONNECTIONS SHALL BE OF FULL PENETRATION WELDS AND WELDED ALL AROUND. a) ALL BEAM AND PIPE SPLICES. b) ALL BEAM FLANGE EXTENSIONS. c) ALL TRUSS MEMBER CONNECTIONS. d) ALL FRAMING BEAM CONNECTIONS. e) ALL OFFSHORE JOINTS. f) ALL TUBULAR CONNECTIONS. ALL OTHER CONNECTIONS SHALL BE FULL STRENGTH WELD (U.N.O)
8.	MINIMUM SIZE OF FILLET WELDS SHALL BE 6 MM UNLESS NOTED OTHERWISE.
9.	DECK PLATING SHALL BE CONTINUOUSLY SEAL WELDED TO THE DECK BEAM FLANGES AND TUBULARS. SEAL WELDING SIZE SHALL BE 4MM.
10.	COAMING ANGLES SHALL BE CONTINUOUSLY SEAL WELDED TO THE DECK PLATING.
11.	COPE DECK PLATING AND SEAL WELD ALL AROUND AT INTERSECTION OF STRUCTURAL MEMBERS.
12.	WALL PLATING SHALL BE CONTINUOUSLY SEAL WELDED TO THE SUPPORTS.
13.	UNLESS NOTED OTHERWISE ALL GRATINGS SHALL BE STITCH WELDED TO SUPPORTING BEAMS.
14.	ALL STITCH WELD SHALL BE MINIMUM 75mm LENGTH.
15.	ALL STRUCTURAL MEMBERS INCLUDING STIFFENERS SHALL BE CUT TO SUIT AND COPE TO FIT UNLESS OTHERWISE SHOWN.
16.	ALL REMOVABLE OR OFFSHORE INSTALLED MEMBERS SHALL BE TEST FITTED AT YARD BEFORE LOAD OUT AND SHALL BE REMOVED AFTER TEST FITTING & MARKED AND DESPATCHED SEPARATELY.
17.	STRUCTURE SHALL BE PAINTED AS PER TENDER SPECIFICATION.
18.	PERIMETERS AROUND CUTOUTS AND PENETRATIONS THROUGH FLOOR CHEQUERED PLATES AND GRATING TO BE REINFORCED.
19.	HOLES PROVIDED IN HANDRAILS DURING GALVANISATION SHALL BE SEALED BY AN APPROVED METHOD AFTER INSTALLATION.
20.	FOR WELDING REFER TENDER SPECIFICATION.
21.	ALL HANDRAIL, SOCKET, GRATING, STAIR TREADS SHALL BE HOT DIP GALVANISED AS PER SPECIFICATION 7-60-801 AND 7-60-802.
22.	FOR TYPICAL WELDING DETAILS REFER STD. NO. 7-60-0807. i.e. DECK WELDING DETAILS.

S.NO.	TRANSPORTATION AND INSTALLATION
1.	ALL COMPONENTS OF THE STRUCTURES SHALL BE PLANNED ASSUMING THE AVAILABILITY OF THE FOLLOWING MINIMUM CONSTRUCTION EQUIPMENT. a) MARINE SPREAD INCLUDING DERRICK BARGE WITH ADEQUATE CRANE CAPACITY. b) CARGO BARGES OF ADEQUATE SIZE/ STABILITY/STRENGTH.
2.	LIFTING EYE SHOWN IN THE DRAWINGS ARE TENTATIVE AND ONLY INDICATE THE PREFERRED SYSTEM.
3.	VERIFICATION OF ALL LIFTING EYES, SPREDER FRAMES LAUNCHING LUG ETC.SHALL BE CARRIED OUT BASED ON APPROVED PROCEDURES FOR FABRICATION/ LOADOUT/ TRANSPORTATION/ INSTALLATION AND STRUCTURAL DESIGN BASIS.
4.	ALL TEMPORARY MEMBERS/COMPONENTS, IF REQUIRED, TO FACILITATE FABRICATION, LOAD-OUT TRANSPORTATION AND INSTALLATION OF THE STRUCTURES SHALL BE PROVIDED AS PER DESIGN.
5.	INSTALLATION AIDS, SUCH AS COUNTER WEIGHTS AND BUMPER GUIDES RIGGING PLATFORMS AND OTHER TEMPORARY MEMBERS NOT INCLUDED IN THE DRAWINGS, SHALL BE DESIGNED AND PROVIDED AS PER REQUIREMENTS.
6.	TEMPORARY TIE DOWN & LIFT BRACES/ COMPONENTS, IF REQUIRED TO FACILITATE FABRICATION, LOADOUT, TRANSPORTION AND INSTALLATION SHALL BE PROVIDED IN ACCORDANCE WITH DESIGN AND SPECIFICATIONS.
7.	PERMANENT MEMBERS SHALL BE CLEANED OF WELD SPLATTER AND TOUCH UP PAINTED AFTER REMOVAL OF ANY TEMPORARY BRACE/COMPONENTS.
8.	DAMAGE OF ANY KIND TO THE PERMANENT STRUCTURES BEFORE AND DURING INSTALLATION AND PRIOR TO HANDOVER SHALL BE COMPLETELY REPAIRED BY AN APPROVED METHOD AND TO THE FULL SATISFACTION OF THE COMPANY.
9.	ALL MEMBERS MARKED "FIELD INSTALLED" SHALL BE INSTALLED "OFFSHORE" AFTER MAKING NECESSARY ADJUSTMENT IN LEVELS, ORIENTATION ETC. TO SUIT SITE CONDITION.

REF. DWG. NO.	REFERENCE DRAWING TITLE

NOTES:

REV.	DATE	REVISIONS	BY	CHKD	APPD.	EE/PC
0	29.01.26	ISSUED FOR TENDER	MUNISH	AA	DP	

ENGINEERS INDIA LIMITED (A Govt. of India Undertaking)

ऑयल एण्ड नेचुरल गैस कारपोरेशन लिमिटेड
OIL AND NATURAL GAS CORPORATION LIMITED

CONSULTANCY SERVICES FOR ENGINEERING DOCUMENT GENERATION FOR WELL PLATFORMS


GENERAL NOTES FOR DECK

SCALE	JOB NO.	UNIT	DIVN.	DEPT	DWG. NO.	REV.
1:1	B774	000	83	43	0001	0


Sht 01 of 02

3-1641-0501 REV.2 A1-841 x 594


B818-002-83-1116[1]

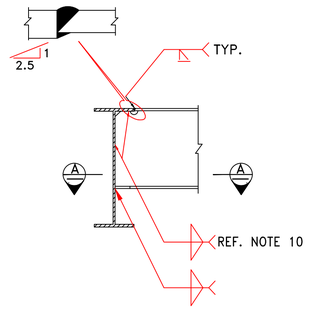


TYP. WELDING DETAIL AT END SUPPORTS OF SECONDARY BEAMS

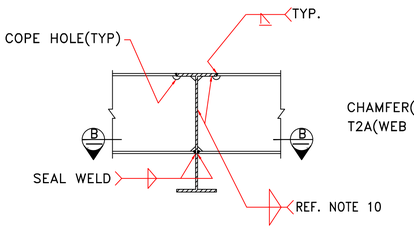

TYP. WELDING DETAIL OF TWO EQUAL SECONDARY BEAMS

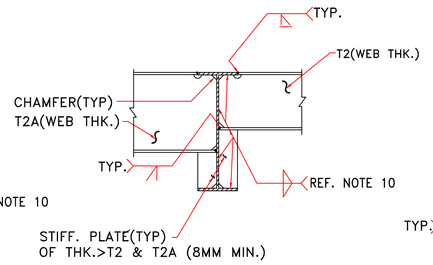



TYP. WELDING DETAIL OF UNEQUAL SECONDARY BEAMS

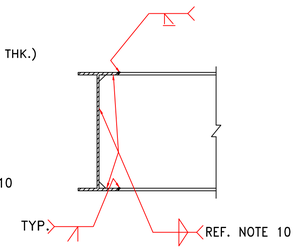


TYP. WELDING DETAIL OF BEAMS OF EQUAL SIZE
(WHEN THERE IS NO TUBULAR CONNECTED AT THE JOINT)

TYP. WELDING DETAILS OF SECONDARY BEAM

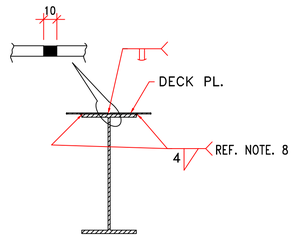


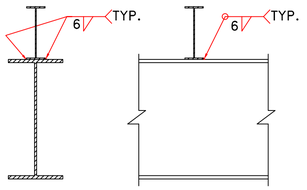


CONNECTION DETAIL OF SECONDARY BEAM TO MAIN BEAM

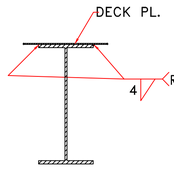


TYP. WELDING DETAIL OF DECK PLATE TO BEAM

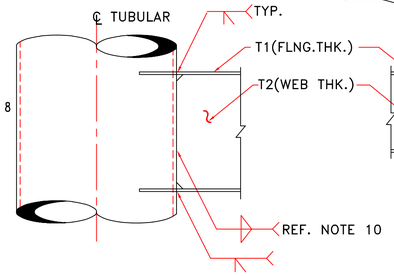


TYP. WELDING DETAIL OF BEAM TO TUBULAR

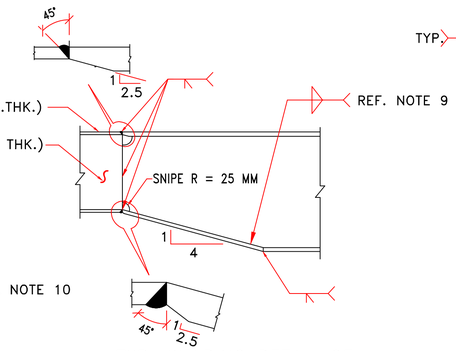


TYP. WELDING DETAIL OF SPLICE FOR BEAMS OF VARYING DEPTH

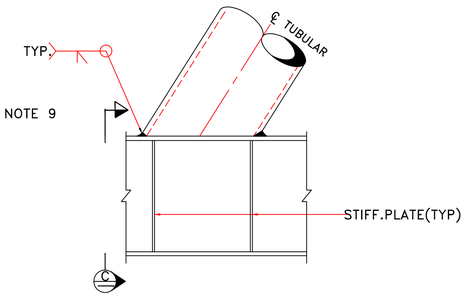


TYP. WELDING DETAIL OF TUBULAR ON BEAM

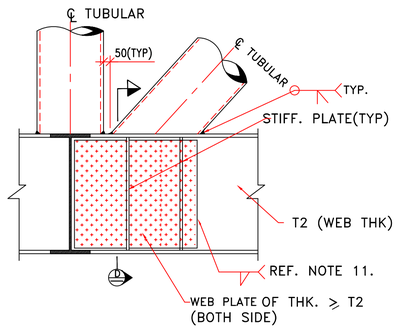


TYP. WELDING DETAIL OF WEB PLATE TO BEAM AND STIFFENER PLATE

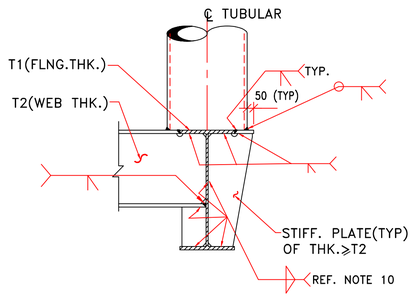


TYP. WELDING DETAIL OF BEAMS OF UNEQUAL SIZE
(WHEN THERE IS TUBULAR CONNECTED AT THE JOINT)

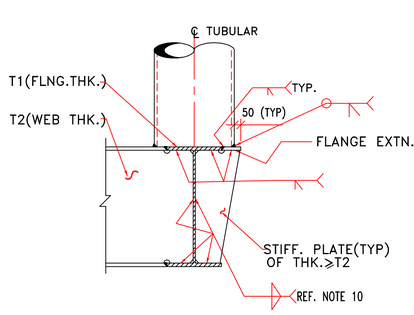


TYP. WELDING DETAIL OF BEAMS OF EQUAL SIZE
(WHEN THERE IS TUBULAR CONNECTED AT THE JOINT)

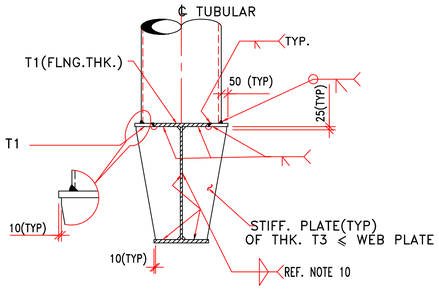


SECTION C

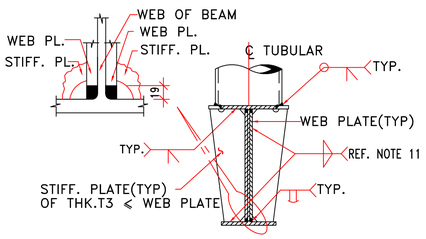


SECTION D

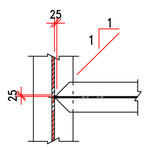


SECTION A

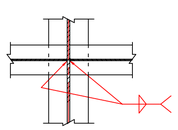

SECTION B

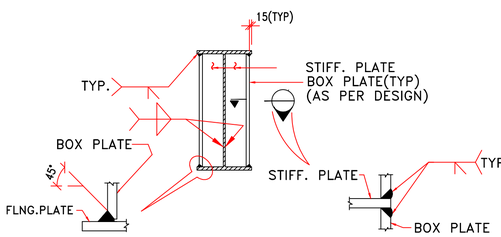

TYP. WELDING DETAIL OF BOX PLATE TO BEAM

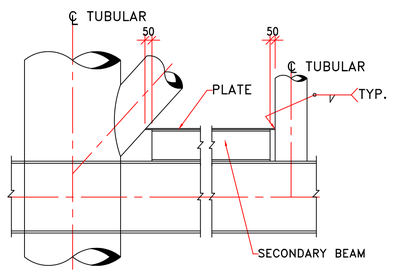

TYPICAL SECONDARY BEAM TERMINATION DETAIL

REF. DWG. NO.	REFERENCE DRAWING TITLE

NOTES:

1. FOR GENERAL NOTES REFER STD. NO. 7-60-0605.
2. ALL WELDING DETAILS TO COMPLY WITH AWS D.1.1 LATEST EDITION, API-RP-2A AND APPROVED WELDING PROCEDURE. ALL FPW SHALL BE BACK GOUGED AND BACK WELDED.
3. FOR TUBULAR TO TUBULAR CONNECTION REFER STD. NO. 7-60-0806.
4. UNLESS NOTED OTHERWISE, THE FOLLOWING CONNECTIONS SHALL BE OF FULL PENETRATION WELDS AND WELDED ALLROUND:
   a) ALL BEAMS ARE PIPE SPLICES
   b) ALL BEAM FLANGE EXTENSIONS
   c) ALL TUBULAR CONNECTIONS
   d) ALL TRUSS MEMBER CONNECTIONS (TUBULAR TO BEAM)
5. MINIMUM SIZE OF FILLET WELDS SHALL BE 6mm UNLESS OTHERWISE SHOWN ON THE DESIGN DRAWINGS (ONLY SEAL WELD SHALL BE OF MIN 4mm)
6. WELD DETAILS DESCRIBED IN THIS DRAWING ARE APPLICABLE UNLESS EXPLICITLY NOTED OTHERWISE ON THE DESIGN DRAWINGS.
7. COPE HOLES/CHAMFERS/SNIPES SHALL BE USED TO ALLOW CONTINUITY OF FULL PENETRATION BUTT WELDS DEPENDING ON FABRICATION REQUIREMENT.
8. CONTINUOUS SEAL WELDING (4mm) SHALL BE APPLIED BETWEEN DECK PLATING AND SECONDARY BEAMS.
9. THE CHOICE OF SINGLE/DOUBLE GROOVE AND WELD POSITION CAN VARY DEPENDING ON WELDING SEQUENCE IT SHALL CONFIRM TO THE WELDING PROCEDURE AND A.W.S. D.1.1.
10. THE DOUBLE FILLET WELD CONNECTING
    a) WEB OF BEAM TO WEB OF BEAM
    b) WEB OF BEAM TO TUBULAR
    c) STIFFENER TO WEB
    d) STIFFENER TO NON LOAD BEARING FLANGE SHALL BE OF SIZE 0.7xCONNECTING ELEMENT SIZE OR 6mm WHICHEVER IS HIGHER.
11. THE FILLET WELD CONNECTING THE WEB PLATE TO THE BEAM AND STIFFENER PLATE WITH WEB PLATE SHALL BE OF SIZE EQUAL TO 0.7 TIMES THE WEB PLATE THICKNESS OR STIFFENER PLATE THICKNESS RESPECTIVELY SUBJECT TO A MINIMUM OF 6mm.

REV.	DATE	REVISIONS	BY	CHKD	APPD	PEMPC
0	29.01.202	ISSUED FOR TENDER	MUNISH	AA	DP	

इंजीनियर्स इंडिया लिमिटेड (भारत सरकार का उपक्रम) ENGINEERS INDIA LIMITED (A Govt. of India Undertaking)

ONGC ओएनजीसी ओॅयल एण्ड नेचुरल गैस कारपोरेशन लिमिटेड
OIL AND NATURAL GAS CORPORATION LIMITED

CONSULTANCY SERVICES FOR ENGINEERING DOCUMENT GENERATION FOR WELL PLATFORMS

DECK WELDING DETAILS


SCALE	JOB NO.	UNIT	DIVN	DEPT	DWG. NO.	REV.
1:1	B774	000	83	43	0001	0

Sht 02 of 02

3-1641-0501 REV.2 A1-841 x 594


यह ड्राइंग एवं इसमें दिए गए डिज़ाइन एवं विवरण इंजीनियर्स इंडिया लिमिटेड की संपत्ति है। इसे उधार देते समय यह समझा जाएगा, न तो इसे पूरा या पूरित किया जाएगा, न ही उपयोग किये जाने वाले अन्य प्रयोग हेतु और न ही उधारकर्ता को लिखित रूप में दी गई सहमति के सिवा उधारकर्ता द्वारा अथवा इसका कोई अन्य प्रयोग हेतु और यह प्रयोग उधार देने वाले द्वारा उधारकर्ता को लिखित रूप में दी गई सहमति के सिवा किसी अन्य प्रयोग के अलावा इसका कोई अन्य प्रयोग किया जाएगा, न प्रदर्शित किया जाएगा और न ही संचित और किसी

B774-101-83-43-0001

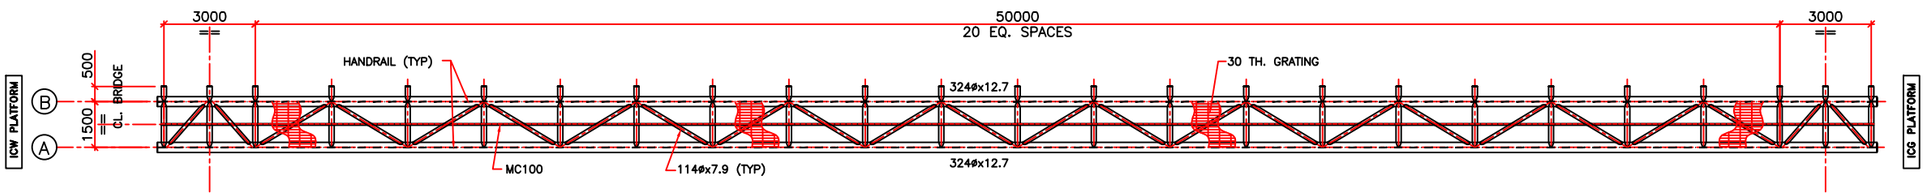


BRIDGE WALKWAY AND HANDRAIL LAYOUT AT TOP CHORD

ALL MEMBERS ARE 168ø x9.27 (U.N.O.)

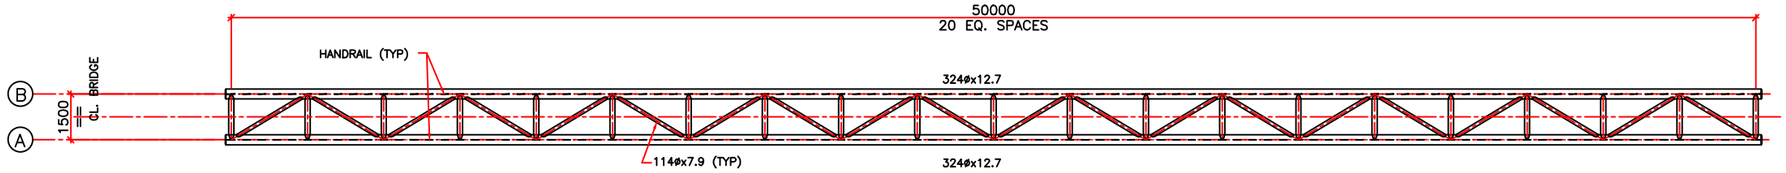


BRIDGE AT BOTTOM CHORD

ALL MEMBERS ARE 168ø x9.27 (U.N.O.)

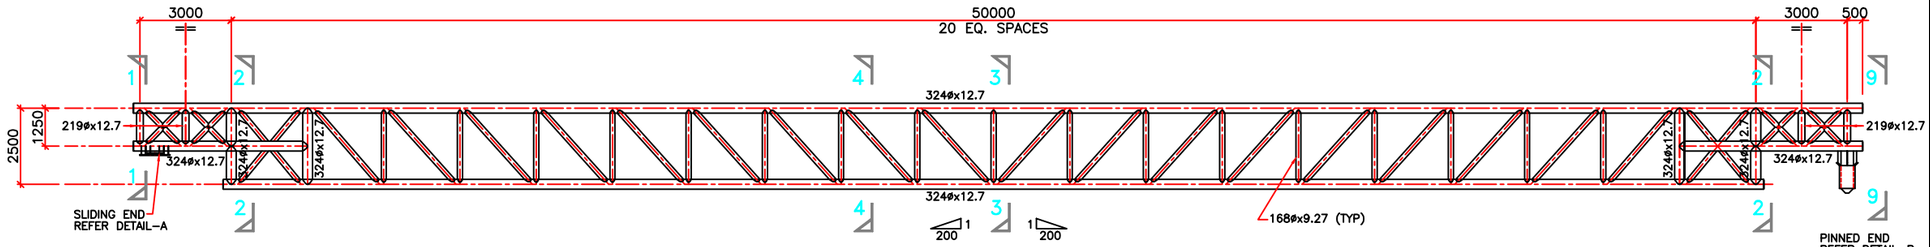


ELEVATION AT ROW A

ALL MEMBERS ARE 168ø x9.5 (U.N.O.)

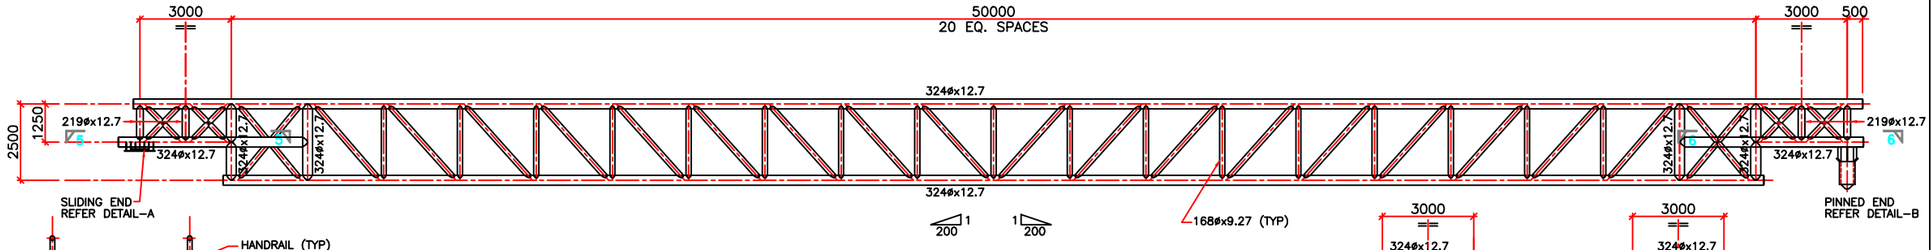


ELEVATION AT ROW B


ALL MEMBERS ARE 168ø x9.5 (U.N.O.)

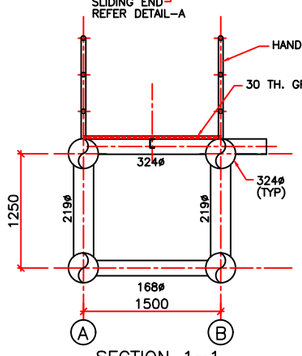


SECTION 1–1

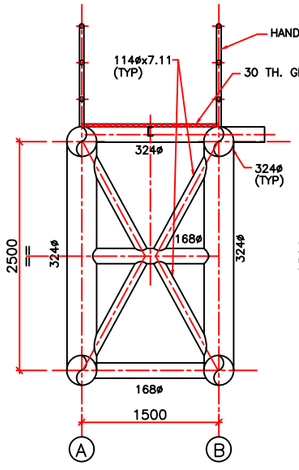


SECTION 2–2

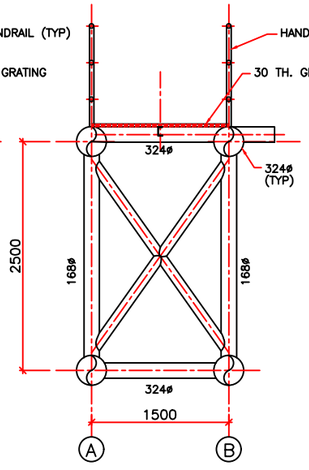


SECTION 3–3

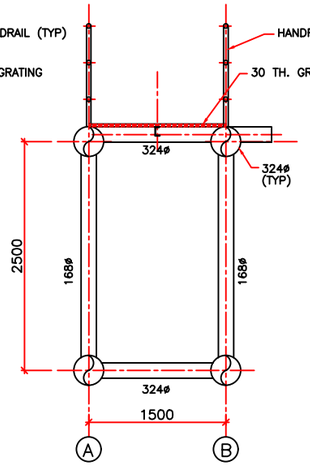

SECTION 4–4

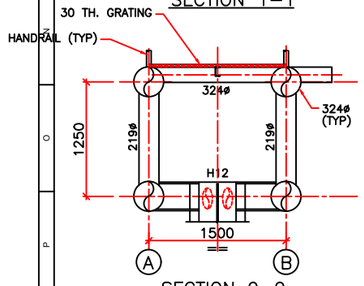


SECTION 9–9

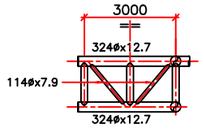


SECTION 5–5

ALL MEMBERS ARE 168ø x9.27 (U.N.O.)

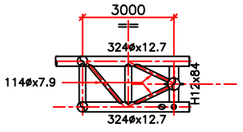


SECTION 6–6


ALL MEMBERS ARE 168ø x9.27 (U.N.O.)

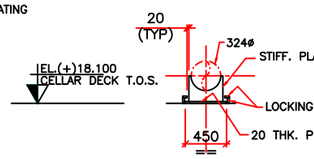


SECTION 7–7

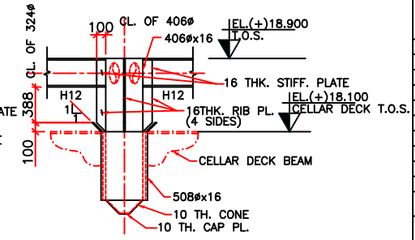

SECTION 8–8

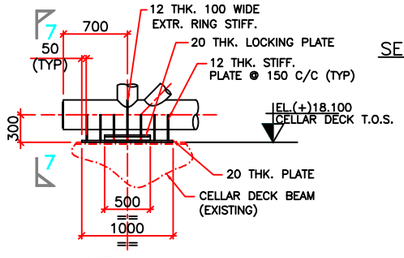

DETAIL–A

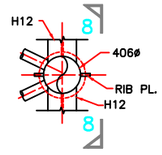

DETAIL–B

NOTES :-

1. DO NOT SCALE THE DRAWING, WORK TO DIMENSIONS ONLY.
2. ALL DIMENSIONS ARE IN MM AND LEVELS ARE IN M U.N.O.
3. ALL ELEVATIONS ARE W.R.T. CHART DATUM (CD) 0.0M CHART DATUM FOR INDIAN WATERS SHALL BE 2.5M BELOW MEAN SEA LEVEL (MSL).
4. MATERIAL SPECIFICATIONS
   a) ALL STIFFENERS, FLANGE EXTENSION PLATES ETC. SHALL BE OF SAME GRADE AS ELEMENT TO WHICH THEY ARE CONNECTED U.N.O.
5. MATERIAL TYPES LISTED IN SC NOS SHALL CONFORM TO ONGC SPEC NO 6001–F.
6. FABRICATOR TO ENSURE MIN 75MM CLEAR GAP B/W HE WELDS FOR CROSS BRACES AND CROSS JOINTS.
7. ALL WELDS SHALL BE FULL PENETRATION WELDS.
8. FOR GRATING REFER EIL STD. 7–60–0802.
9. FOR HANDRAIL REFER EIL STD. 7–60–0801.

- ALL DETAILS, DIMENSIONS, LEVELS & MEMBER SIZES IN THE DRAWING ARE INDICATIVE AND ARE PROVIDED FOR BIDDERS UNDERSTANDING OF SCOPE OF WORK ONLY.ALL DETAILS SHOWN IN THE DRAWING SHALL BE VERIFIED BY CONTRACTOR DURING PRE–ENGINEERING SURVEY & DETAIL ENGINEERING SHALL BE CARRIED OUT BY CONTRACTOR FOR EXECUTION OF WORKS.
- ALL THE DIMENSIONS ARE IN MM AND LEVELS ARE IN METER (U.N.O.)

ISSUED FOR TENDER

REF. DWG. NO.	REFERENCE DRAWING TITLE
ICG–DG–MD–104	LOWER DECK FRAMING PLAN
ICG–DG–MD–105	ELEVATION ROW A & B
ICG–DG–MD–106	ELEVATION ROW 1 & 2
ICG–DG–MD–107	ELEVATION ROW 3 & 4
ICW–70–052	LOWER DECK FRAMING PLAN
ICW–70–056	ICW PLATFORM DECK ELEVATION AT ROW A & B
ICW–70–057	ICW PLATFORM DECK ELEVATION AT ROW 1,2,3 & 4

FOR TENDER PURPOSE ONLY

REV.	DATE	REVISIONS	BY	CHKD	APPD	PEM/PC
0	10.10.25	ISSUED FOR BIDS	MUNISH	AA	DP	

ENGINEERS INDIA LIMITED (A Govt. of India Undertaking)

ऑयल एण्ड नेचुरल गैस कारपोरेशन लिमिटेड
OIL AND NATURAL GAS CORPORATION LIMITED

एम एन संपत्तियों की मौजूदा पुल का नवीकरण/प्रदलाव

REFURBISHMENT/REPLACEMENT OF EXISTING BRIDGE AT MH ASSET

आई सी डबलू से आई सी जी के निचली छत पुल का सामान्य विन्यास एवं ब्यौरा


G.A. AND DETAILS OF ICW TO ICG LOWER DECK BRIDGE

SCALE	JOB NO.	UNIT	DIVN.	DEPT.	DWG. NO.	REV.
1:150	B774	101	83	43	0001	A


3-1641-0501 REV.2 A1-841x594

प्रस्तुत आरेख एवं इसमें निहित डिज़ाइन वैशिष्ट्यों ईंडिया इंजीनियर्स लिमिटेड की संपत्ति है। ये मात्र उधार दिए गए हैं और उधारकर्ता ने यह स्पष्ट समझौता किया है कि न तो इन्हें पुनः मुद्रित किया जाएगा, न नकल की जाएगी, न उधार दिए जाएंगे, न प्रतिलिपि किए जाएंगे और न ही सीमित और निजी प्रयोग के अलावा इनका किसी अन्य प्रयोग होगा और यह प्रयोग उधार देने वाले द्वारा उधारकर्ता को लिखित रूप में दी गई सहमति से होगा।
The drawing, design and details given on this format are the property of ENGINEERS INDIA LIMITED. They are merely loaned on the borrower's express agreement that they will not be reproduced, copied, exhibited or used, except in the limited way permitted by a written consent given by the lender to the borrower for the intended use.


B774-101-83-43-0002

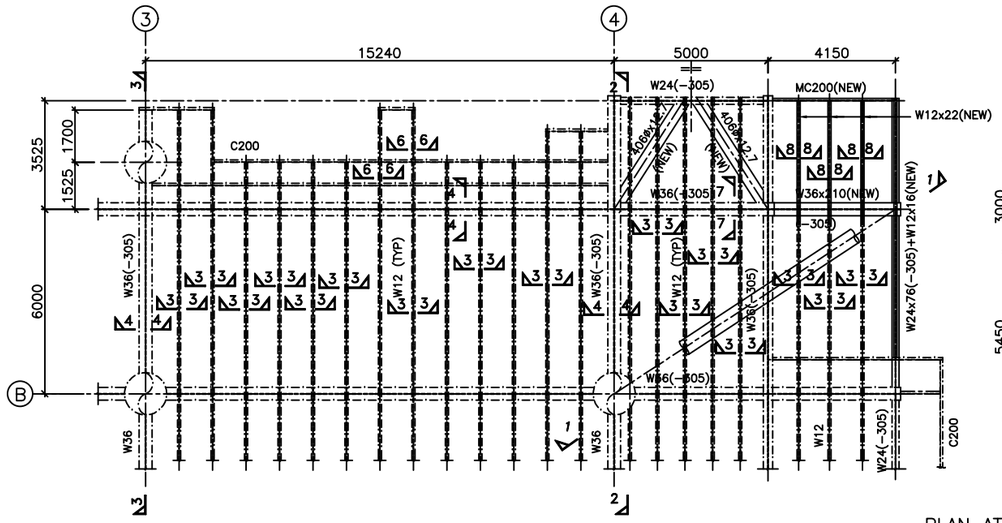

PLAN AT EL(+)18.300 (T.O.S.)

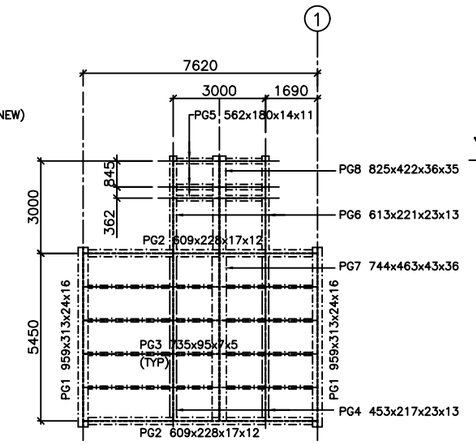

PLAN AT LQ LEVEL AT BRIDGE LANDING AREA EL(+)27.750 (T.O.S.)

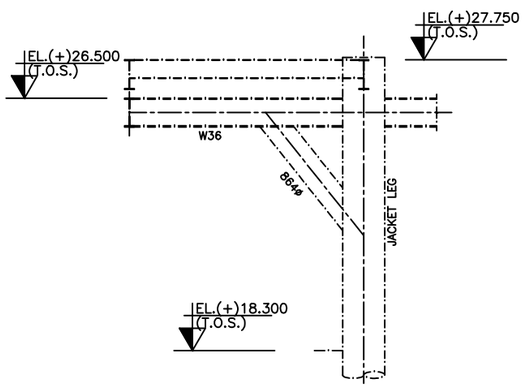

PART ELEVATION OF ROW B


REF. DWG. NO.	REFERENCE DRAWING TITLE
ICW-70-050 TO ICW-70-059	ICW PLATFORM DECK DRWAINGS

NOTES :-


1. DO NOT SCALE THE DRAWING, WORK TO DIMENSIONS ONLY.
2. ALL DIMENSIONS ARE IN MM AND LEVELS ARE IN M U.N.O.
3. ALL ELEVATIONS ARE W.R.T. CHART DATUM (CD) 0.0M CHART DATUM FOR INDIAN WATERS SHALL BE 2.5M BELOW MEAN SEA LEVEL (MSL).
4. MATERIAL SPECIFICATIONS
   a) ALL STIFFENERS, FLANGE EXTENSION PLATES ETC. SHALL BE OF SAME / HIGHER GRADE AS ELEMENT TO WHICH THEY ARE CONNECTED U.N.O.
5. MATERIAL TYPES LISTED IN SC NOS SHALL CONFORM TO ONGC SPEC 6001 F.
6. FABRICATOR TO ENSURE MIN 75MM CLEAR GAP B/W HE WELDS FOR CROSS BRACES AND CROSS JOINTS.
7. ALL WELDS SHALL BE FULL PENETRATION WELDS.
8. FOR GRATING REFER EIL STD. 7-60-0802.
9. FOR HANDRAIL REFER EIL STD. 7-60-0801.

- ALL DETAILS, DIMENSIONS, LEVELS & MEMBER SIZES IN THE DRAWING ARE INDICATIVE AND ARE PROVIDED FOR BIDDERS UNDERSTANDING OF SCOPE OF WORK ONLY.ALL DETAILS SHOWN IN THE DRAWING SHALL BE VERIFIED BY CONTRACTOR DURING PRE-ENGINEERING SURVEY & DETAIL ENGINEERING SHALL BE CARRIED OUT BY CONTRACTOR FOR EXECUTION OF WORKS.
- ALL THE DIMENSIONS ARE IN MM AND LEVELS ARE IN METER (U.N.O.)


ISSUED FOR TENDER

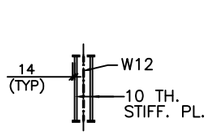


SECTION 3-3

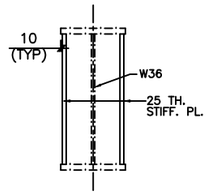


SECTION 4-4

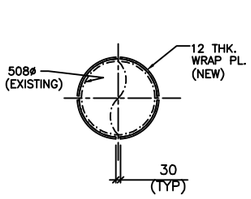


SECTION 5-5

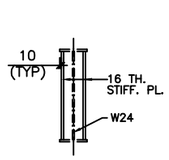


SECTION 6-6

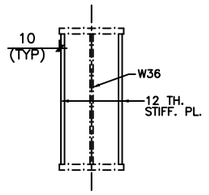


SECTION 7-7

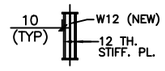


SECTION 8-8

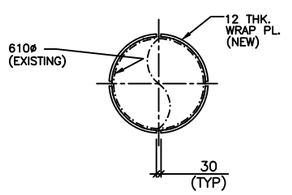


SECTION 9-9

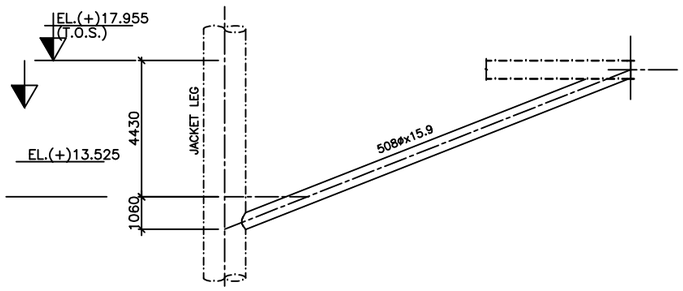

SECTION 1-1

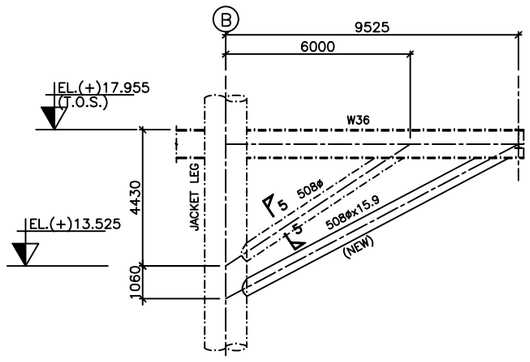

SECTION 2-2

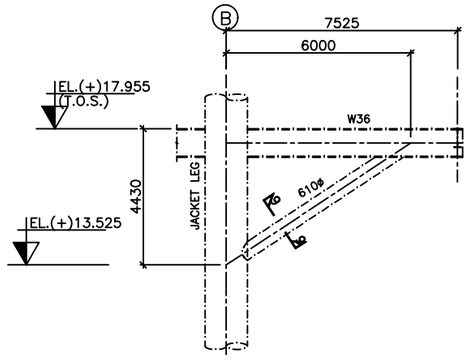

SECTION 3-3

REV.	DATE	REVISIONS	BY	CHKD	APPD	PEMPC
A	01.12.25	ISSUED FOR TENDER	MUNISH	AMS	DP	

इंजीनियर्स इंडिया लिमिटेड ENGINEERS INDIA LIMITED (A Govt. of India Undertaking)

ऑयल एण्ड नेचुरल गैस कारपोरेशन लिमिटेड
OIL AND NATURAL GAS CORPORATION LIMITED

REFURBISHMENT/REPLACEMENT OF BRIDGES IN MH ASSET


STRENGTHENING OF ICW UPPER DECK

SCALE	JOB NO.	UNIT	DIVN.	DEPT.	DWG. NO.	REV.
1:100	B774	101	83	43	0002	A


प्रस्तुत आरेख एवं इसमें निहित डिजाइन इंजीनियर्स इंडिया लिमिटेड की संपत्ति है। ये मात्र उधार दिए गए है और इसको किसी अन्य प्रयोग हेतु जाएंगे और न ही संपत्ति और किसी प्रयोग के अलावा इसका कार्य अन्य प्रयोग हेतु जाएंगे और न ही संपत्ति और किसी प्रयोग उधार देने वाले द्वारा उधारकर्ता को लिखित रूप से दी गई सहमति से होगा।
The drawing, design and details given on this format are the property of ENGINEERS INDIA LIMITED. They are merely loaned on the borrower's express agreement that they will not be reproduced, copied, exhibited or used, except in the limited way permitted by a written consent given by the lender to the borrower for the intended use.

3-1641-0501 REV.2 A1-841x594


B774-101-83-43-0003

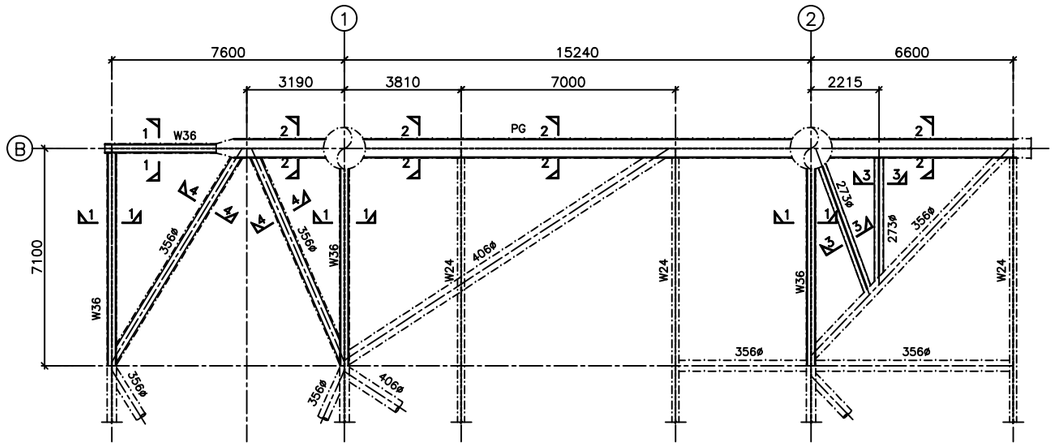


PART PLAN OF MAIN DECK AT EL(+)26.500 (T.O.S.)

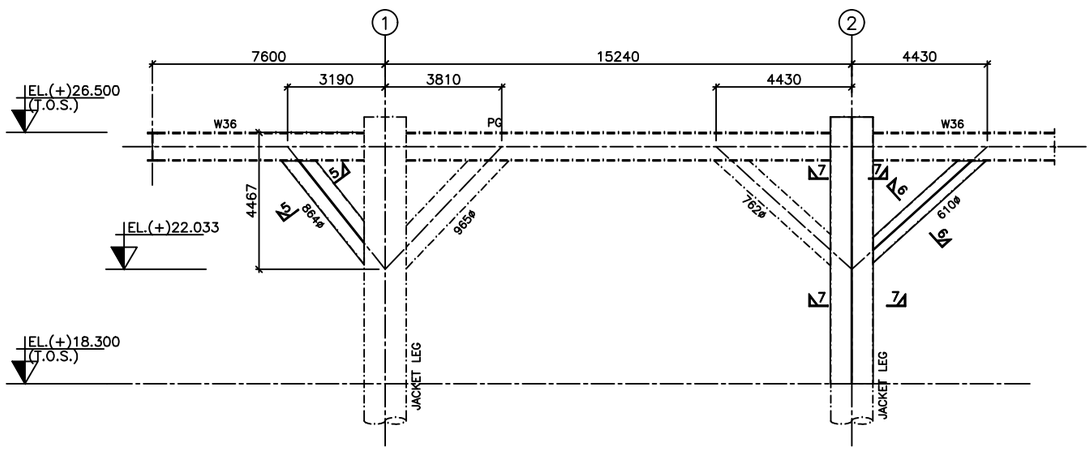


PART ELEVATION OF ROW B

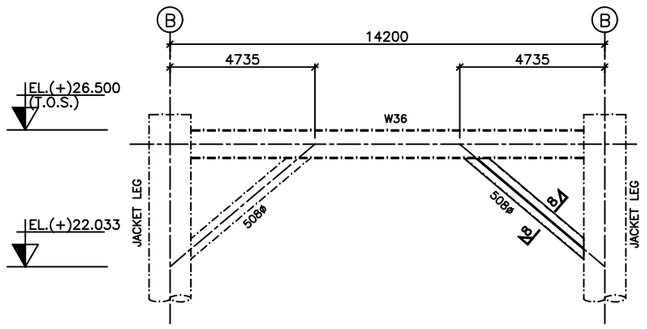


PART ELEVATION OF ROW 2

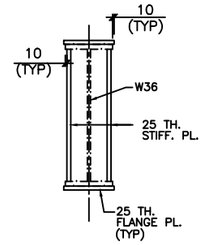


SECTION 1–1

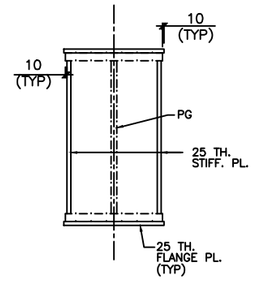


SECTION 2–2

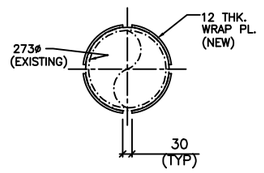


SECTION 3–3

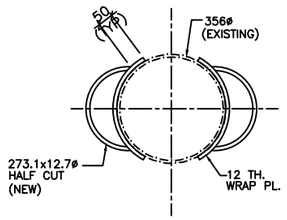


SECTION 4–4

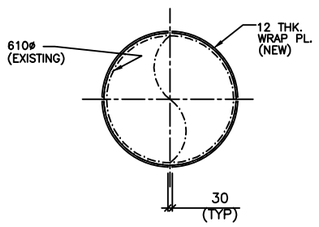


SECTION 5–5

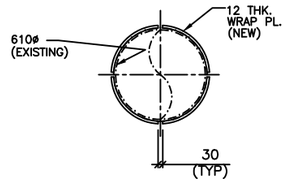

SECTION 6–6

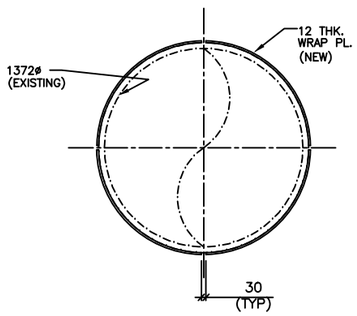

SECTION 7–7

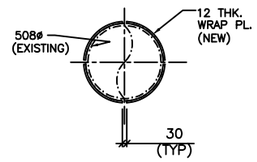

SECTION 8–8

REF. DWG. NO.	REFERENCE DRAWING TITLE
ICW-70-050 TO ICW-70-059	ICW PLATFORM DECK DRWAINGS

NOTES :-

1. DO NOT SCALE THE DRAWING, WORK TO DIMENSIONS ONLY.
2. ALL DIMENSIONS ARE IN MM AND LEVELS ARE IN M U.N.O.
3. ALL ELEVATIONS ARE W.R.T. CHART DATUM (CD) 0.0M CHART DATUM FOR INDIAN WATERS SHALL BE 2.5M BELOW MEAN SEA LEVEL (MSL).
4. MATERIAL SPECIFICATIONS
   a) ALL STIFFENERS, FLANGE EXTENSION PLATES ETC. SHALL BE OF SAME / HIGHER GRADE AS ELEMENT TO WHICH THEY ARE CONNECTED U.N.O.
5. MATERIAL TYPES LISTED IN SC NOS SHALL CONFORM TO ONGC SPEC 6001 F.
6. FABRICATOR TO ENSURE MIN 75MM CLEAR GAP B/W HE WELDS FOR CROSS BRACES AND CROSS JOINTS.
7. ALL WELDS SHALL BE FULL PENETRATION WELDS.
8. FOR GRATING REFER EIL STD. 7–60–0802.
9. FOR HANDRAIL REFER EIL STD. 7–60–0801.

* ALL DETAILS, DIMENSIONS, LEVELS & MEMBER SIZES IN THE DRAWING ARE INDICATIVE AND ARE PROVIDED FOR BIDDERS UNDERSTANDING OF SCOPE OF WORK ONLY.ALL DETAILS SHOWN IN THE DRAWING SHALL BE VERIFIED BY CONTRACTOR DURING PRE–ENGINEERING SURVEY & DETAIL ENGINEERING SHALL BE CARRIED OUT BY CONTRACTOR FOR EXECUTION OF WORKS.
* ALL THE DIMENSIONS ARE IN MM AND LEVELS ARE IN METER (U.N.O.)

ISSUED FOR TENDER

REV.	DATE	REVISIONS	BY	CHKD	APPD	PEM/PC
A	01.12.25	ISSUED FOR TENDER	MUNISH	AMS	DP	

इंजीनियर्स इंडिया लिमिटेड ENGINEERS INDIA LIMITED (A Govt. of India Undertaking)

ऑयल एण्ड नेचुरल गैस कारपोरेशन लिमिटेड
OIL AND NATURAL GAS CORPORATION LIMITED

REFURBISHMENT/REPLACEMENT OF BRIDGES IN MH ASSET

STRENGTHENING OF ICW UPPER DECK


SCALE	JOB NO.	UNIT	DIVN.	DEPT.	DWG. NO.	REV.
1:100	B774	101	83	43	0003	A

प्रस्तुत आरेख एवं इसमें निहित डिज़ाइन इंजीनियर्स इंडिया लिमिटेड की संपत्ति है। ये मात्र उधार दिए गए है और न तो इन्हें पुनः मुद्रित किया जाएगा, न नकल की जाएगी, न उधार दिए जाएंगे, न प्रदर्शित किए जाएंगे और न ही संलिप्त और किसी प्रयोग के अलावा इनका कोई अन्य प्रयोग होगा और यह प्रयोग उधार देने वाले द्वारा इंजीनियर्स को लिखित रूप में दी गई सहमति से होगा ।


The drawing, design and details given on this format are the property of ENGINEERS INDIA LIMITED. They are merely loaned on the borrower's express agreement that they will not be reproduced, copied, exhibited or used, except in the limited way permitted by a written consent given by the lender to the borrower for the intended use.

B774-101-83-43-0004


यह ड्राइंग डिज़ाइन एवं इसमें निहित विवरण इंजीनियर्स इंडिया लिमिटेड की संपत्ति है। ये मात्र उधार दिए गए हैं और उधारकर्ता ने यह स्पष्ट समझौता किया है कि न तो इन्हें पुनः तैयार किया जाएगा, न नकल की जाएगी, न उधार दिए जाएंगे, न प्रतिलिपि किए जाएंगे और न ही सार्वजनिक और किसी प्रयोग के अलावा इनका उपयोग इनके मूल अन्य प्रयोग होगा और यह प्रयोग उधार देने वाले द्वारा उधारकर्ता को लिखित रूप में दी गई सहमति से होगा।
The drawing, design and details given on this format are the property of ENGINEERS INDIA LIMITED. They are merely loaned on the borrower's express agreement that they will not be reproduced, copied, exhibited or used, except in the limited way permitted by a written consent given by the lender to the borrower for the intended use.

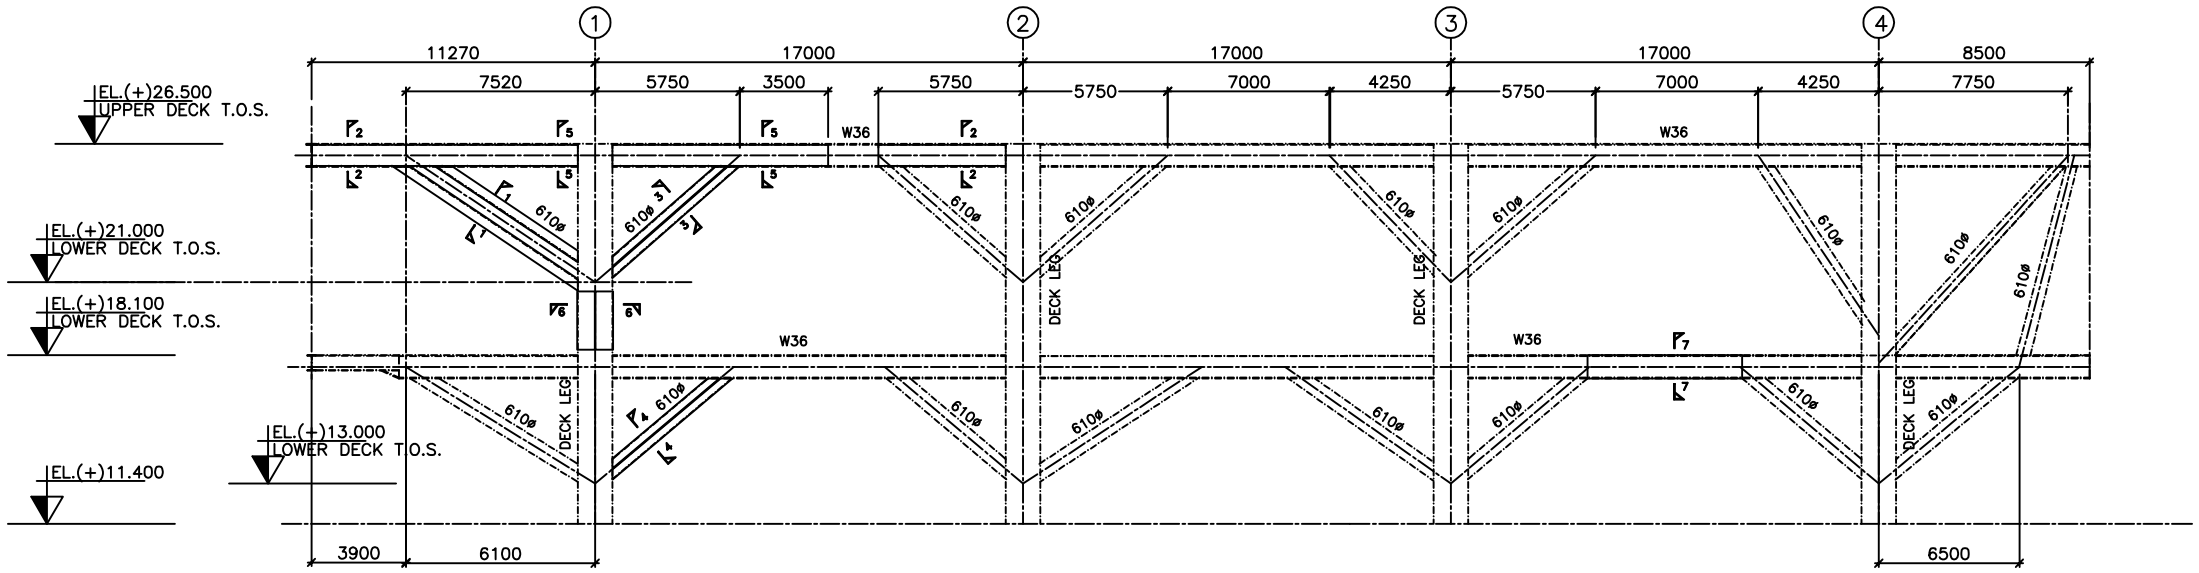


ELEVATION OF DECK ROW A

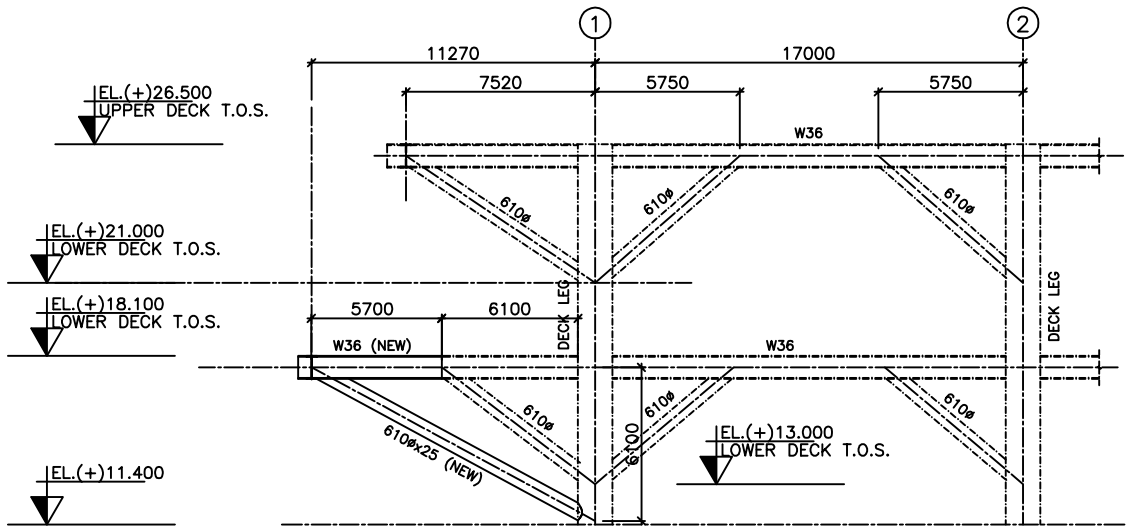


PART ELEVATION OF DECK ROW B

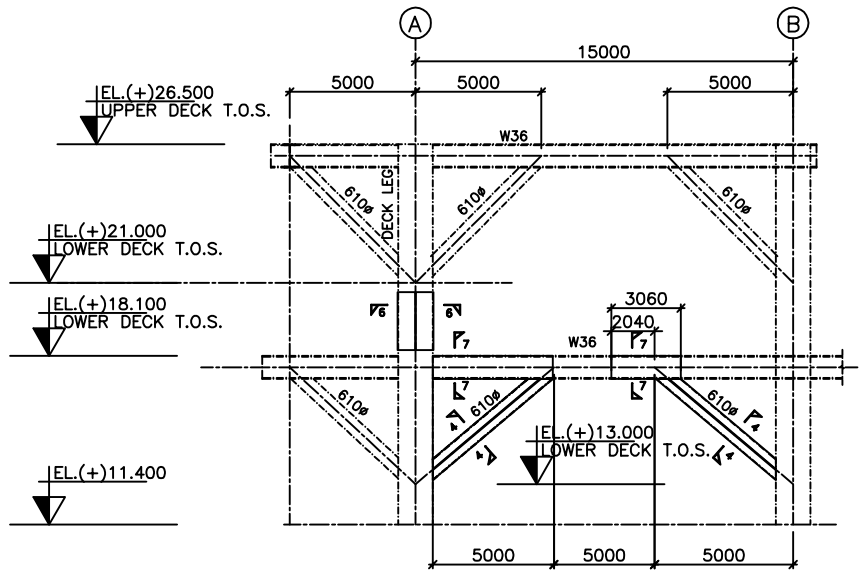


PART ELEVATION OF DECK ROW 1

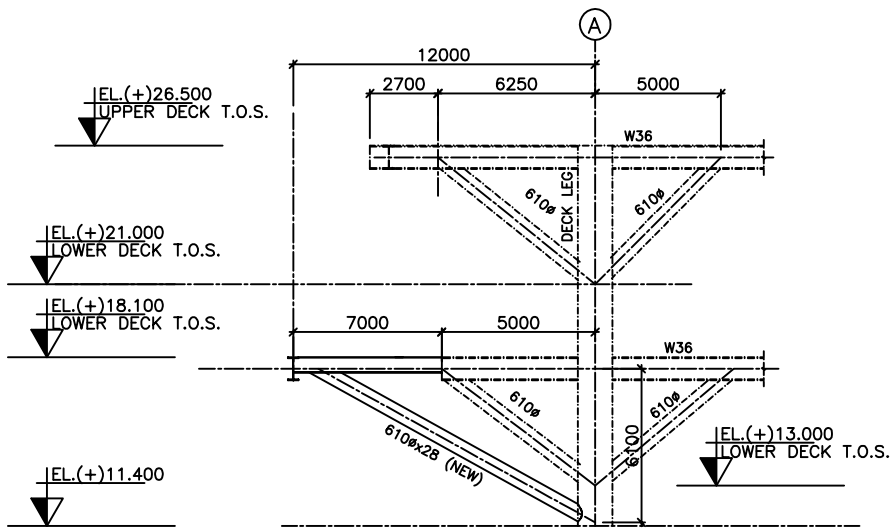


PART ELEVATION OF DECK ROW 3

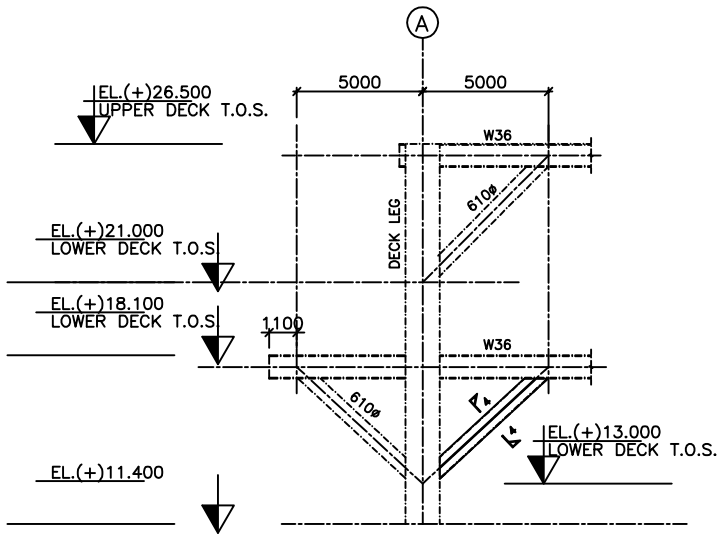


PART ELEVATION OF DECK ROW 2

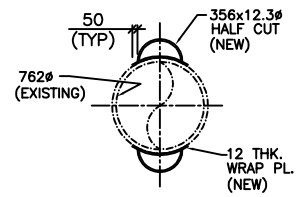


SECTION 1–1

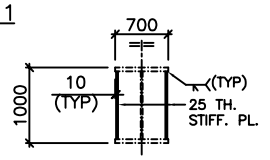


SECTION 2–2

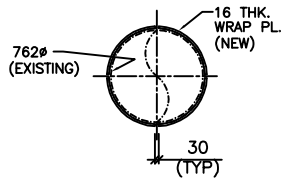


SECTION 3–3

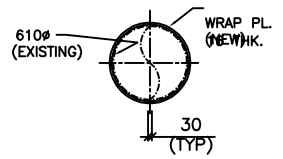


SECTION 4–4

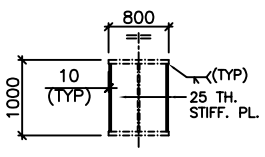

SECTION 5–5

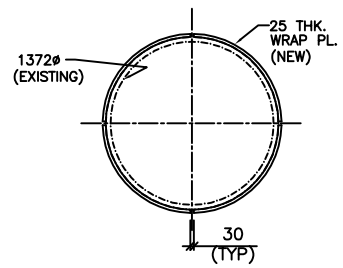

SECTION 6–6

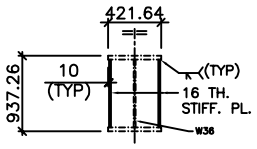

SECTION 7–7

REF. DWG. NO.	REFERENCE DRAWING TITLE
ICG-DD-MD-103 TO 108	ICG DECK DRAWINGS

NOTES :-

1. DO NOT SCALE THE DRAWING, WORK TO DIMENSIONS ONLY.
2. ALL DIMENSIONS ARE IN MM AND LEVELS ARE IN M U.N.O.
3. ALL ELEVATIONS ARE W.R.T. CHART DATUM (CD) 0.0M CHART DATUM FOR INDIAN WATERS SHALL BE 2.5M BELOW MEAN SEA LEVEL (MSL).
4. MATERIAL SPECIFICATIONS
   a) ALL STIFFENERS, FLANGE EXTENSION PLATES ETC. SHALL BE OF SAME / HIGHER GRADE AS ELEMENT TO WHICH THEY ARE CONNECTED U.N.O.
5. MATERIAL TYPES LISTED IN SC NOS SHALL CONFORM TO ONGC SPEC 6001 F.
6. FABRICATOR TO ENSURE MIN 75MM CLEAR GAP B/W HE WELDS FOR CROSS BRACES AND CROSS JOINTS.
7. ALL WELDS SHALL BE FULL PENETRATION WELDS.
8. FOR GRATING REFER EIL STD. 7–60–0802.
9. FOR HANDRAIL REFER EIL STD. 7–60–0801.

* ALL DETAILS, DIMENSIONS, LEVELS & MEMBER SIZES IN THE DRAWING ARE INDICATIVE AND ARE PROVIDED FOR BIDDERS UNDERSTANDING OF SCOPE OF WORK ONLY.ALL DETAILS SHOWN IN THE DRAWING SHALL BE VERIFIED BY CONTRACTOR DURING PRE–ENGINEERING SURVEY & DETAIL ENGINEERING SHALL BE CARRIED OUT BY CONTRACTOR FOR EXECUTION OF WORKS.
* ALL THE DIMENSIONS ARE IN MM AND LEVELS ARE IN METER (U.N.O.)

ISSUED FOR TENDER

REV.	DATE	REVISIONS	BY	CHKD	APPD	PEM/PC
A	09.12.25	ISSUED FOR TENDER	MUNISH	AP	DP	

इंजीनियर्स इंडिया लिमिटेड ENGINEERS INDIA LIMITED (A Govt. of India Undertaking)


ऑयल एण्ड नेचुरल गैस कारपोरेशन लिमिटेड
OIL AND NATURAL GAS CORPORATION LIMITED

REFURBISHMENT/REPLACEMENT OF BRIDGES IN MH ASSET

ICG LANDING AREA-MODIFICATIONS


SCALE	JOB NO.	UNIT	DIVN.	DEPT.	DWG. NO.	REV.
1:100	B774	101	83	43	0004	A

3-1641-0501 REV.2 A1-841x594

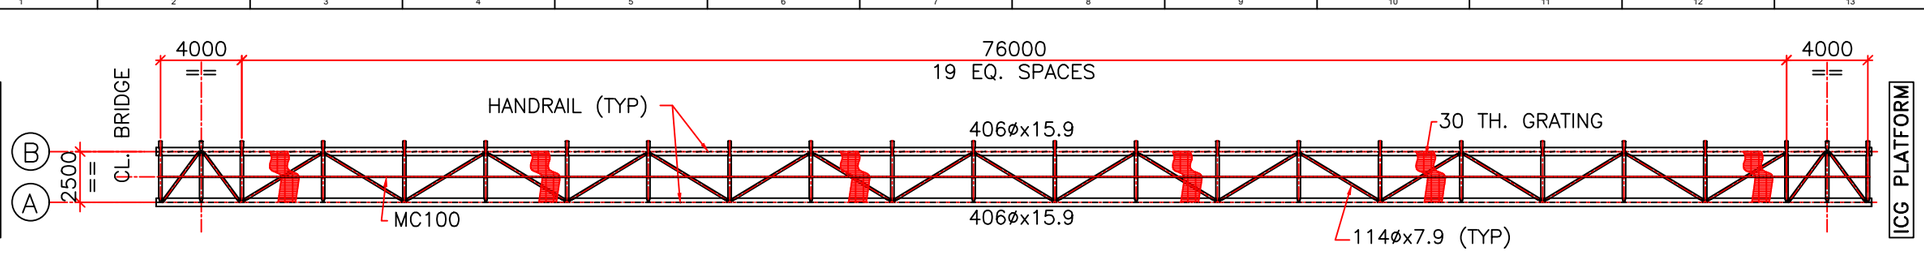


BRIDGE WALKWAY AND HANDRAIL LAYOUT AT TOP CHORD

ALL MEMBERS ARE 168ø x9.27 (U.N.O.)

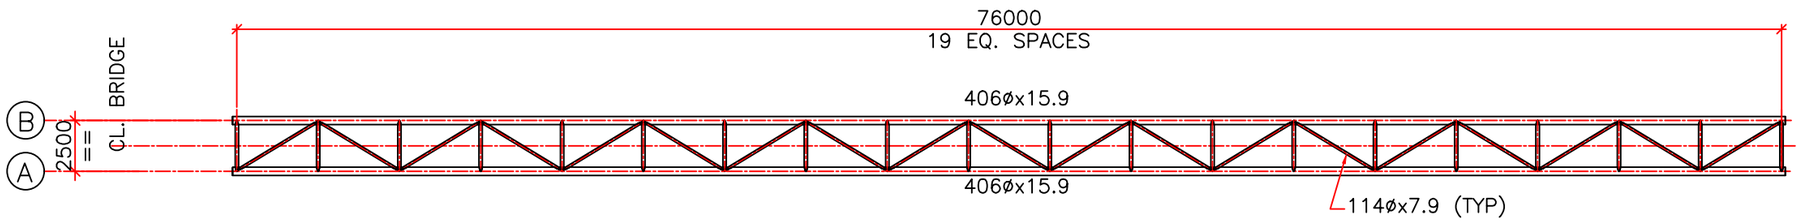


BRIDGE AT BOTTOM CHORD

ALL MEMBERS ARE 168ø x9.27 (U.N.O.)

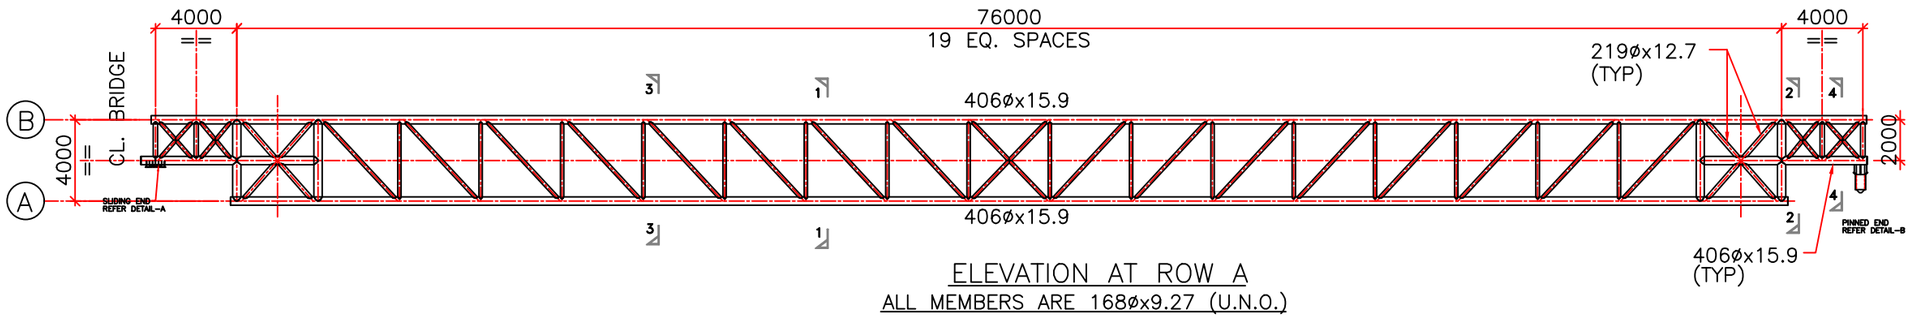


ELEVATION AT ROW A

ALL MEMBERS ARE 168ø x9.27 (U.N.O.)

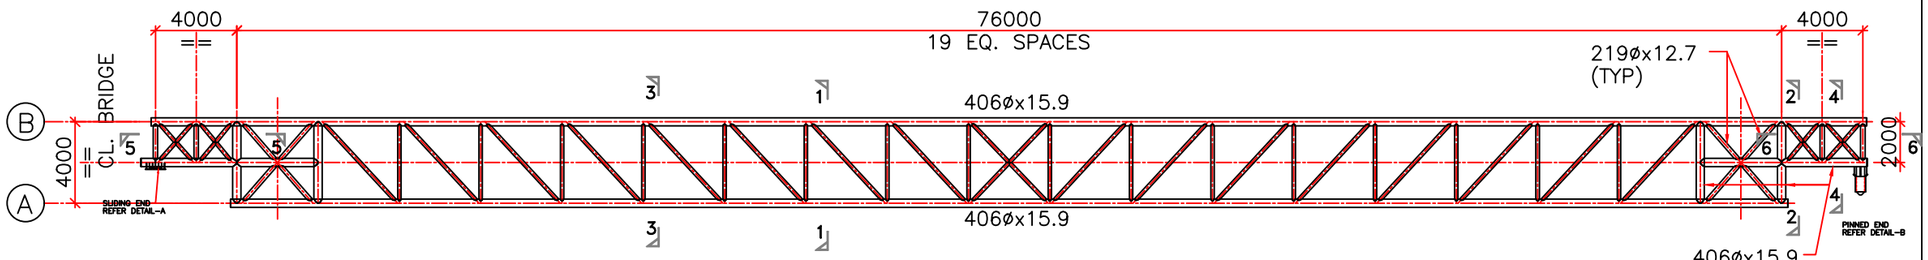


ELEVATION AT ROW B

ALL MEMBERS ARE 168ø x9.27 (U.N.O.)

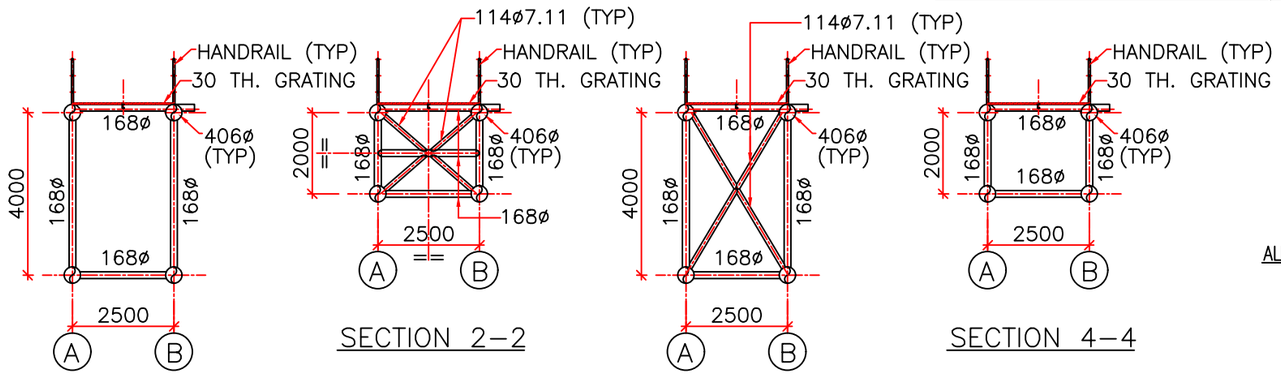

SECTION 1–1 | SECTION 2–2 | SECTION 3–3 | SECTION 4–4

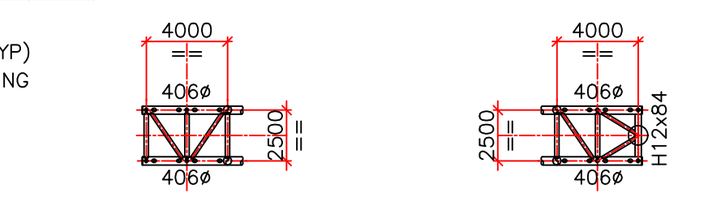

SECTION 5–5 | SECTION 6–6

ALL MEMBERS ARE 168ø x9.27 (U.N.O.)

REF. DWG. NO.	REFERENCE DRAWING TITLE

NOTES :-

1. DO NOT SCALE THE DRAWING, WORK TO DIMENSIONS ONLY.
2. ALL DIMENSIONS ARE IN MM AND LEVELS ARE IN M U.N.O.
3. ALL ELEVATIONS ARE W.R.T. CHART DATUM (CD) 0.0M CHART DATUM FOR INDIAN WATERS SHALL BE 2.5M BELOW MEAN SEA LEVEL (MSL).
4. MATERIAL SPECIFICATIONS
   a) ALL STIFFENERS, FLANGE EXTENSION PLATES ETC. SHALL BE OF SAME GRADE AS ELEMENT TO WHICH THEY ARE CONNECTED U.N.O.
5. MATERIAL TYPES LISTED IN SC NOS SHALL CONFORM TO ONGC SPEC 6001 F.
6. FABRICATOR TO ENSURE MIN 75MM CLEAR GAP B/W HE WELDS FOR CROSS BRACES AND CROSS JOINTS.
7. ALL WELDS SHALL BE FULL PENETRATION WELDS.
8. FOR GRATING REFER EIL STD. 7-60-0802.
9. FOR HANDRAIL REFER EIL STD. 7-60-0801.

- ALL DETAILS, DIMENSIONS, LEVELS & MEMBER SIZES IN THE DRAWING ARE INDICATIVE AND ARE PROVIDED FOR BIDDERS UNDERSTANDING OF SCOPE OF WORK ONLY.ALL DETAILS SHOWN IN THE DRAWING SHALL BE VERIFIED BY CONTRACTOR DURING PRE-ENGINEERING SURVEY & DETAIL ENGINEERING SHALL BE CARRIED OUT BY CONTRACTOR FOR EXECUTION OF WORKS.
- ALL THE DIMENSIONS ARE IN MM AND LEVELS ARE IN METER (U.N.O.)

ISSUED FOR TENDER

REV.	DATE	REVISIONS	BY	CHKD	APPD	PEM/PC
A	09.10.25	ISSUED FOR BIDS	MUNISH	AP	DP	

इंजीनियर्स इंडिया लिमिटेड ENGINEERS INDIA LIMITED (A Govt. of India Undertaking)

ऑयल एण्ड नेचुरल गैस कारपोरेशन लिमिटेड
OIL AND NATURAL GAS CORPORATION LIMITED


एन एच संपत्ति की मौजूदा पुल का नवीकरण-बदलाव	REFURBISHMENT/REPLACEMENT OF EXISTING BRIDGE AT MH ASSET
आई सी पु से आई सी जी के निचली छत पुल का सामान्य विन्यास एवं ब्योरा	G.A. AND DETAILS OF ICP TO ICG LOWER DECK BRIDGE

SCALE	JOB NO.	UNIT	DIVN.	DEPT.	DWG. NO.	REV.
1:225	B774	102	83	43	0001- sht 1 of 2	A


3-1641-0501 REV.2 A1-841x594

प्रस्तुत आरेख एवं इसमें निहित डिजाइन इंजीनियर्स इंडिया लिमिटेड की संपत्ति है । ये मात्र उधार दिए गए हैं और उधारकर्ता ने यह स्पष्ट समझौता किया है कि न तो उन्हें पुन: मुद्रित किया जाएगा, न नकल की जाएगी, न उधार दिए जाएंगे, न प्रदर्शित किए जाएंगे और न ही लिखित अनुमति के अलावा इनका किसी प्रयोग के लिए उपयोग किया जाएगा ।
The drawing, design and details given on this format are the property of ENGINEERS INDIA LIMITED. They are merely loaned on the borrower's express agreement that they will not be reproduced, copied, exhibited or used, except in the limited way permitted by a written consent given by the lender to the borrower for the intended use.


B774-102-83-43-0001

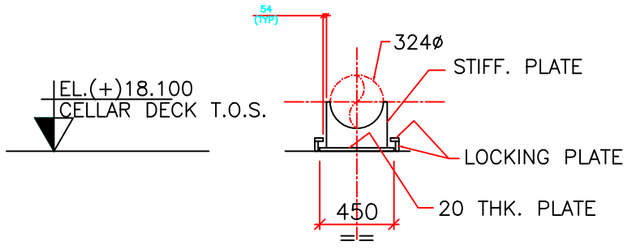


SECTION 7–7

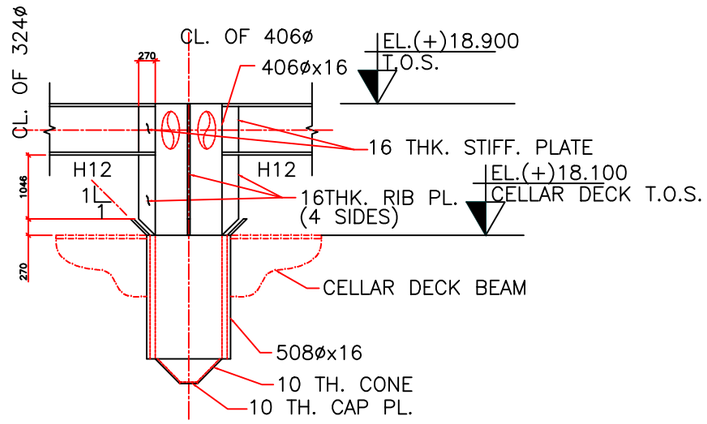

SECTION 8–8

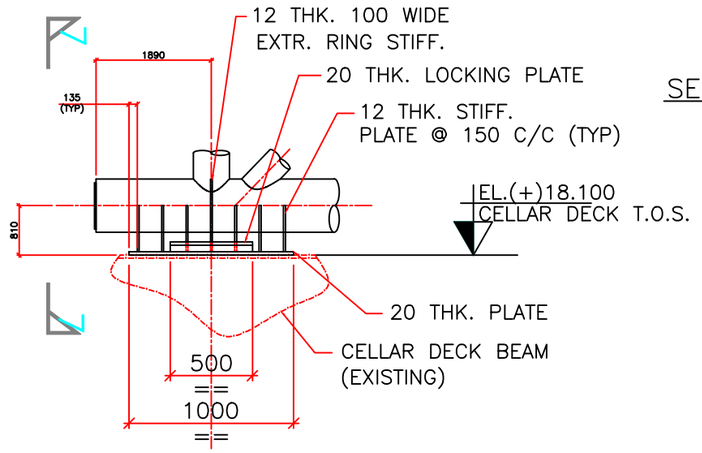

DETAIL–A

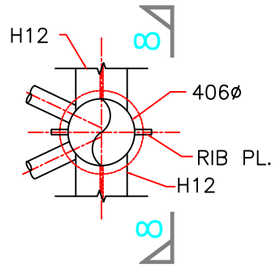

DETAIL–B

REF. DWG. NO.	REFERENCE DRAWING TITLE

NOTES :-

1. DO NOT SCALE THE DRAWING, WORK TO DIMENSIONS ONLY.
2. ALL DIMENSIONS ARE IN MM AND LEVELS ARE IN M U.N.O.
3. THE DRAWING SHALL BE READ IN CONJUNCTION WITH SHT 1 OF 2

- ALL DETAILS, DIMENSIONS, LEVELS & MEMBER SIZES IN THE DRAWING ARE INDICATIVE AND ARE PROVIDED FOR BIDDERS UNDERSTANDING OF SCOPE OF WORK ONLY.ALL DETAILS SHOWN IN THE DRAWING SHALL BE VERIFIED BY CONTRACTOR DURING PRE-ENGINEERING SURVEY. & DETAIL ENGINEERING SHALL BE CARRIED OUT BY CONTRACTOR FOR EXECUTION OF WORKS.
- ALL THE DIMENSIONS ARE IN MM AND LEVELS ARE IN METER (U.N.O.)

ISSUED FOR TENDER

REV.	DATE	REVISIONS	BY	CHKD	APPD	PEM/PC
A	09.10.25	ISSUED FOR BIDS	MUNISH	AP	DP	

इंजीनियर्स इंडिया लिमिटेड ENGINEERS INDIA LIMITED (A Govt. of India Undertaking)

ऑयल एण्ड नेचुरल गैस कारपोरेशन लिमिटेड
OIL AND NATURAL GAS CORPORATION LIMITED


एम एच संपत्तियों की मौजूदा पुल का नवीकरण/बदलाव	REFURBISHMENT/REPLACEMENT OF EXISTING BRIDGE AT MH ASSET
आई सी पी से आई सी जी के निचली छत पुल का सामान्य विन्यास एवं ब्यौरा	G.A. AND DETAILS OF ICP TO ICG LOWER DECK BRIDGE

SCALE	JOB NO.	UNIT	DIVN.	DEPT.	DWG. NO.	REV.
1:225	B774	102	83	43	0001- sht 2 of 2	A


प्रस्तुत आरेख एवं इसमें निहित डिजाइन इंजीनियर्स इंडिया लिमिटेड की संपत्ति है। ये मात्र उधार दिए गए हैं और इन्हें पुनः वापिस किया जाएगा, न नकल की जाएगी, न उधार दिए जाएंगे, न प्रदर्शित किए जाएंगे और न ही बीमित की किसी प्रयास के अलावा इनका कोई अन्य प्रयोग किया जाएगा और यह प्रयोग उधार देने वाले द्वारा उधारकर्ता को लिखित रूप में दी गई सहमति से होना ।

The drawing, design and details given on this format are the property of ENGINEERS INDIA LIMITED. They are merely loaned on the borrower's express agreement that they will not be reproduced, copied, exhibited or used, except in the limited way permitted by a written consent given by the lender to the borrower for the intended use.


B774-102-83-43-0002

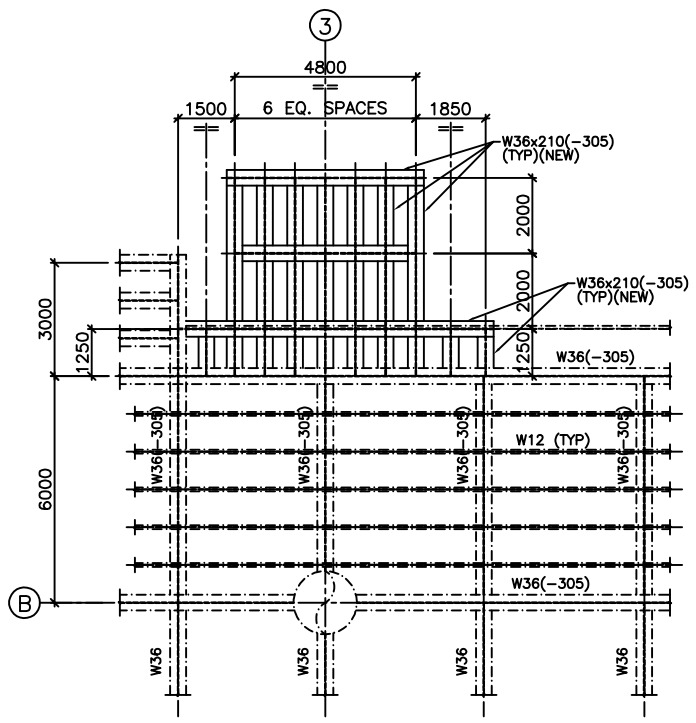


PART PLAN AT EL(+)18.500 (T.O.S.)

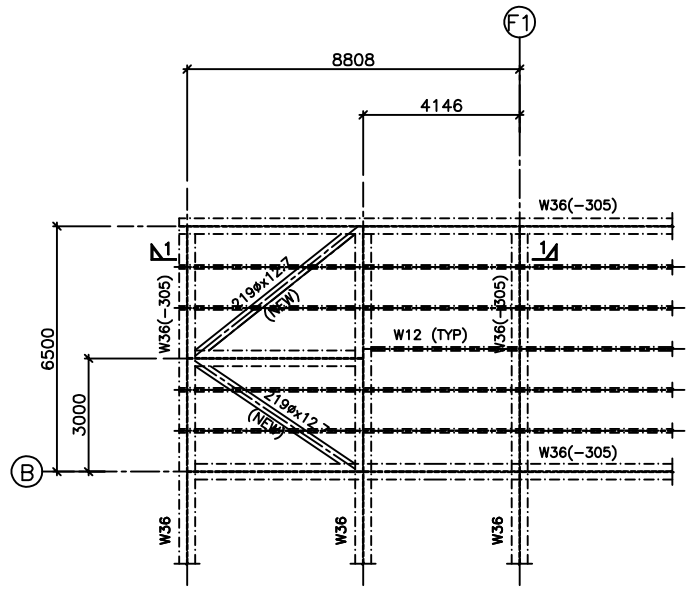


PART PLAN AT EL(+)18.500 (T.O.S.)

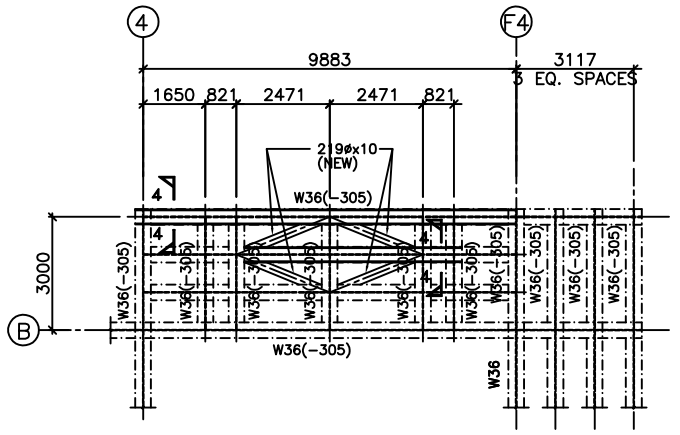


PART PLAN AT EL(+)26.500 (T.O.S.)

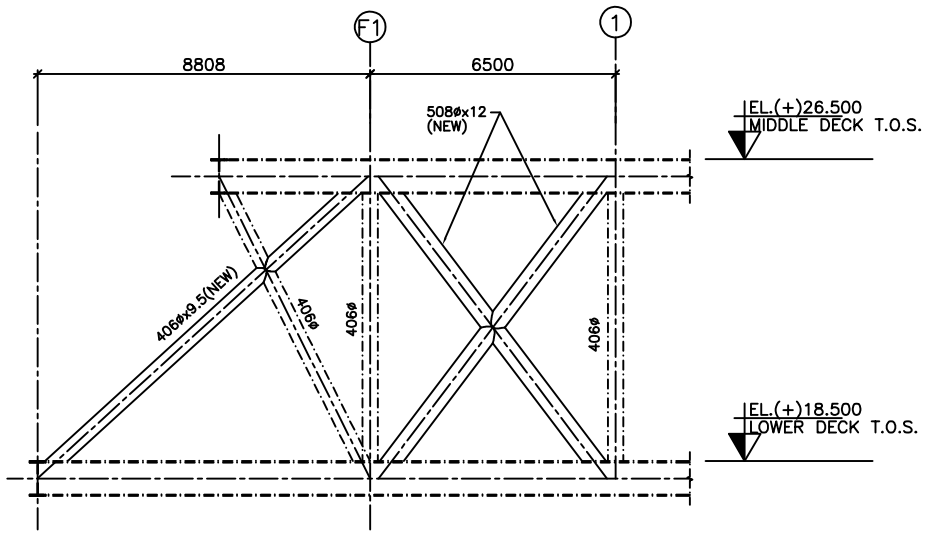


SECTION 1–1

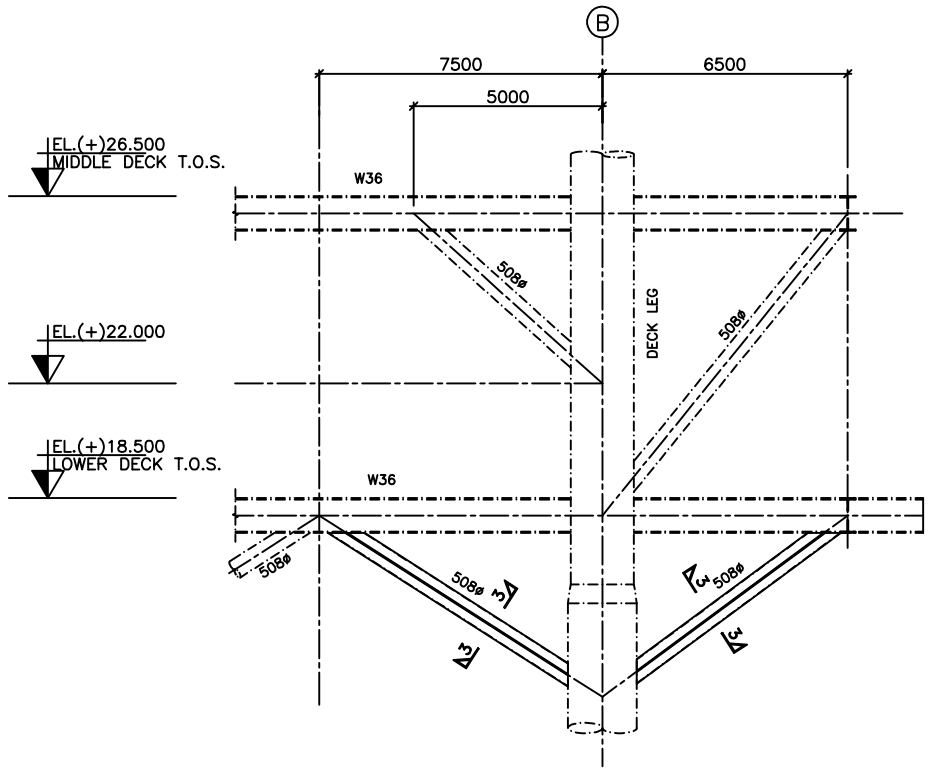


PART ELEVATION OF DECK ROW 1

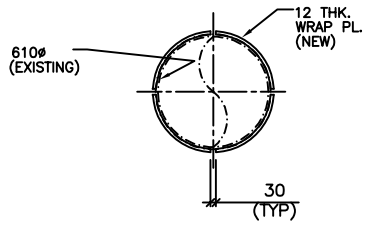


SECTION 2–2

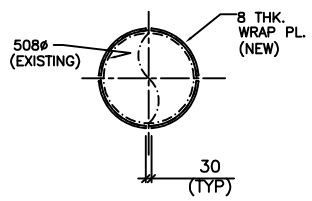


SECTION 3–3

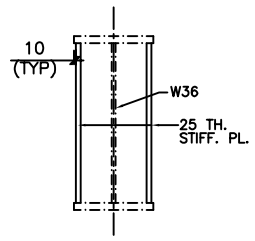

SECTION 4–4

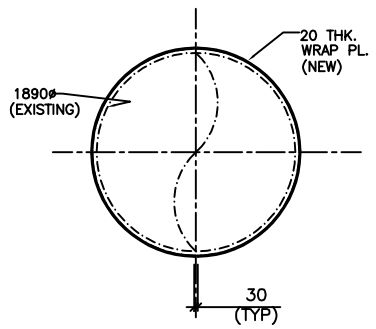

SECTION 5–5

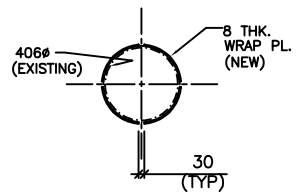

SECTION 6–6

REF. DWG. NO.	REFERENCE DRAWING TITLE
ICP-70-050 TO ICP-70-062	ICP PLATFORM DECK DRAWINGS

NOTES :-

1. DO NOT SCALE THE DRAWING, WORK TO DIMENSIONS ONLY.
2. ALL DIMENSIONS ARE IN MM AND LEVELS ARE IN M U.N.O.
3. ALL ELEVATIONS ARE W.R.T. CHART DATUM (CD) 0.0M CHART DATUM FOR INDIAN WATERS SHALL BE 2.5M BELOW MEAN SEA LEVEL (MSL).
4. MATERIAL SPECIFICATIONS
   a) ALL STIFFENERS, FLANGE EXTENSION PLATES ETC. SHALL BE OF SAME / HIGHER GRADE AS ELEMENT TO WHICH THEY ARE CONNECTED U.N.O.
5. MATERIAL TYPES LISTED IN SC NOS SHALL CONFORM TO ONGC SPEC 6001 F.
6. FABRICATOR TO ENSURE MIN 75MM CLEAR GAP B/W HE WELDS FOR CROSS BRACES AND CROSS JOINTS.
7. ALL WELDS SHALL BE FULL PENETRATION WELDS.
8. FOR GRATING REFER EIL STD. 7-60-0802.
9. FOR HANDRAIL REFER EIL STD. 7-60-0801.

* ALL DETAILS, DIMENSIONS, LEVELS & MEMBER SIZES IN THE DRAWING ARE INDICATIVE AND ARE PROVIDED FOR BIDDERS UNDERSTANDING OF SCOPE OF WORK ONLY.ALL DETAILS SHOWN IN THE DRAWING SHALL BE VERIFIED BY CONTRACTOR DURING PRE-ENGINEERING SURVEY & DETAIL ENGINEERING SHALL BE CARRIED OUT BY CONTRACTOR FOR EXECUTION OF WORKS.
* ALL THE DIMENSIONS ARE IN MM AND LEVELS ARE IN METER (U.N.O.)

ISSUED FOR TENDER

REV.	DATE	REVISIONS	BY	CHKD	APPD	PEM/PC
A	01.12.25	ISSUED FOR TENDER	MUNISH	AP	DP	

इंजीनियर्स इंडिया लिमिटेड ENGINEERS INDIA LIMITED (A Govt. of India Undertaking)

ऑयल एण्ड नेचुरल गैस कारपोरेशन लिमिटेड
OIL AND NATURAL GAS CORPORATION LIMITED

REFURBISHMENT/REPLACEMENT OF BRIDGES IN MH ASSET


ICP LANDING AREA -MODIFICATIONS

SCALE	JOB NO.	UNIT	DIVN.	DEPT.	DWG. NO.	REV.
1:100	B774	102	83	43	0002	A


3-1641-0501 REV.2 A1-841x594

प्रस्तुत आरेख एवं इसमें निहित डिजाइन इंजीनियर्स इंडिया लिमिटेड की संपत्ति है। ये मात्र उधार दिए गए हैं और उधार दिए गए उद्देश्य के अलावा इनका कोई अन्य उपयोग नहीं अन्य प्रयोग होगा और यह प्रयोग उधार देने वाले द्वारा उधारकर्ता को लिखित रूप में दी गई सहमति से होगा।
The drawing, design and details given on this format are the property of ENGINEERS INDIA LIMITED. They are merely loaned on the borrower's express agreement that they will not be reproduced, copied, exhibited or used, except in the limited way permitted by a written consent given by the lender to the borrower for the intended use.


B774-102-83-43-0003

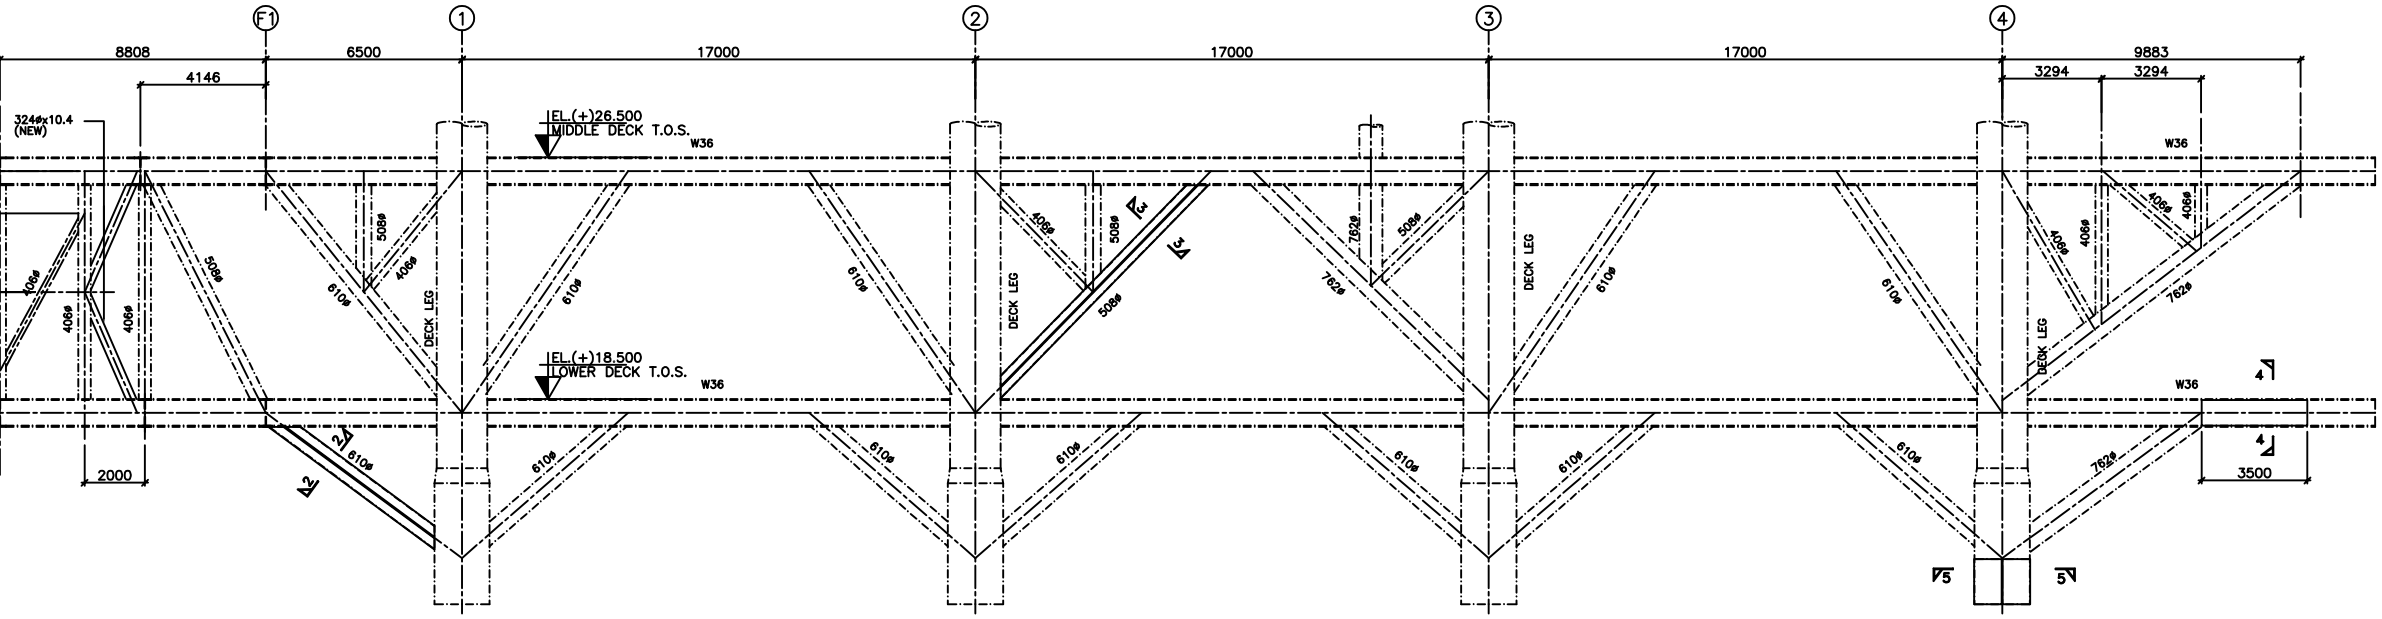


PART ELEVATION OF DECK ROW B

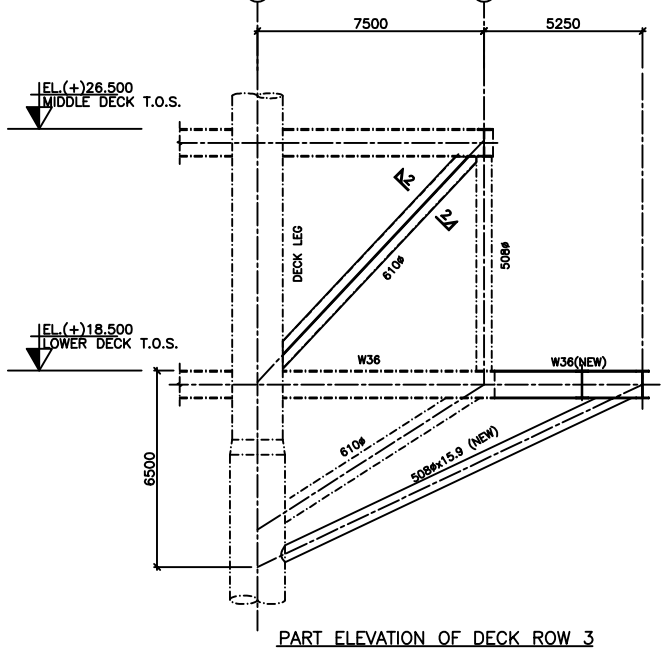


PART ELEVATION OF DECK ROW 3

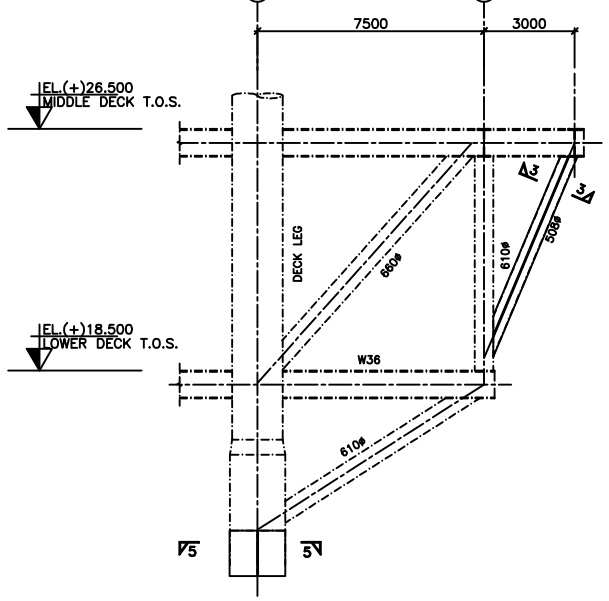

PART ELEVATION OF DECK ROW 4

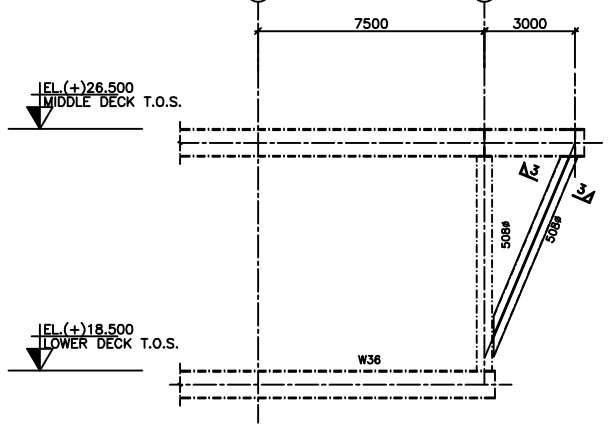

PART ELEVATION OF DECK ROW F4

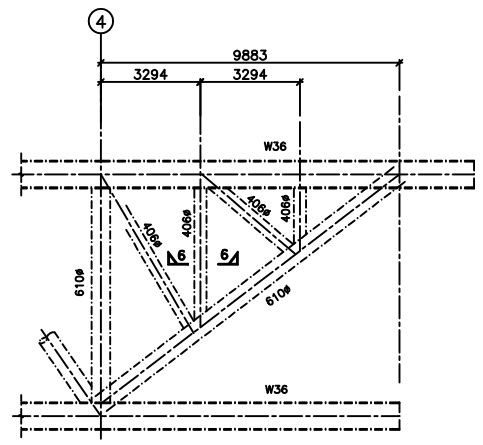

PART ELEVATION OF DECK ROW FB

REF. DWG. NO.	REFERENCE DRAWING TITLE
ICP-70-050 TO ICP-70-062	ICP PLATFORM DECK DRAWINGS

NOTES :-

1. DO NOT SCALE THE DRAWING, WORK TO DIMENSIONS ONLY.
2. ALL DIMENSIONS ARE IN MM AND LEVELS ARE IN M U.N.O.
3. ALL ELEVATIONS ARE W.R.T. CHART DATUM (CD) 0.0M CHART DATUM FOR INDIAN WATERS SHALL BE 2.5M BELOW MEAN SEA LEVEL (MSL).
4. MATERIAL SPECIFICATIONS
   a) ALL STIFFENERS, FLANGE EXTENSION PLATES ETC. SHALL BE OF SAME / HIGHER GRADE AS ELEMENT TO WHICH THEY ARE CONNECTED U.N.O.
5. MATERIAL TYPES LISTED IN SC NOS SHALL CONFORM TO ONGC SPEC 6001 F.
6. FABRICATOR TO ENSURE MIN 75MM CLEAR GAP B/W HE WELDS FOR CROSS BRACES AND CROSS JOINTS.
7. ALL WELDS SHALL BE FULL PENETRATION WELDS.
8. FOR GRATING REFER EIL STD. 7-60-0802.
9. FOR HANDRAIL REFER EIL STD. 7-60-0801.

* ALL DETAILS, DIMENSIONS, LEVELS & MEMBER SIZES IN THE DRAWING ARE INDICATIVE AND ARE PROVIDED FOR BIDDERS UNDERSTANDING OF SCOPE OF WORK ONLY.ALL DETAILS SHOWN IN THE DRAWING SHALL BE VERIFIED BY CONTRACTOR DURING PRE-ENGINEERING SURVEY & DETAIL ENGINEERING SHALL BE CARRIED OUT BY CONTRACTOR FOR EXECUTION OF WORKS.
* ALL THE DIMENSIONS ARE IN MM AND LEVELS ARE IN METER (U.N.O.)

ISSUED FOR TENDER

REV.	DATE	REVISIONS	BY	CHKD	APPD	PEM/PC
A	01.12.25	ISSUED FOR TENDER	MUNISH	AP	DP	

ENGINEERS INDIA LIMITED (A Govt. of India Undertaking)

ऑयल एण्ड नेचुरल गैस कारपोरेशन लिमिटेड
OIL AND NATURAL GAS CORPORATION LIMITED

REFURBISHMENT/REPLACEMENT OF BRIDGES IN MH ASSET

ICP LANDING AREA- MODIFICATIONS


SCALE	JOB NO.	UNIT	DIVN.	DEPT.	DWG. NO.	REV.
1:125	B774	102	83	43	0003	A

3-1641-0501 REV.2 A1-841x594


प्रस्तुत आरेख एवं इसमें निहित डिज़ाइन इंजीनियर्स इंडिया लिमिटेड की संपत्ति है कि न तो उन्हें पुनः मुद्रित किया जाएगा, न नकल की जाएगी, न उधार दिए गए हैं और उधारकर्ता ने यह स्पष्ट समझौता किया है कि न तो उन्हें पुनः मुद्रित किया जाएगा, न नकल की जाएगी, न उधार दिए जाएंगे, न प्रयोग किए जाएंगे और न ही सीमित और किसी प्रयोग के अलावा इसका कोई अन्य प्रयोग होगा और यह प्रयोग उधार देने वाले द्वारा उधारकर्ता को लिखित रूप में दी गई सहमति से होगा ।

The drawing, design and details given on this format are the property of ENGINEERS INDIA LIMITED. They are merely loaned on the borrower's express agreement that they will not be reproduced, copied, exhibited or used, except in the limited way permitted by a written consent given by the lender to the borrower for the intended use.


B774-102-83-43-0004

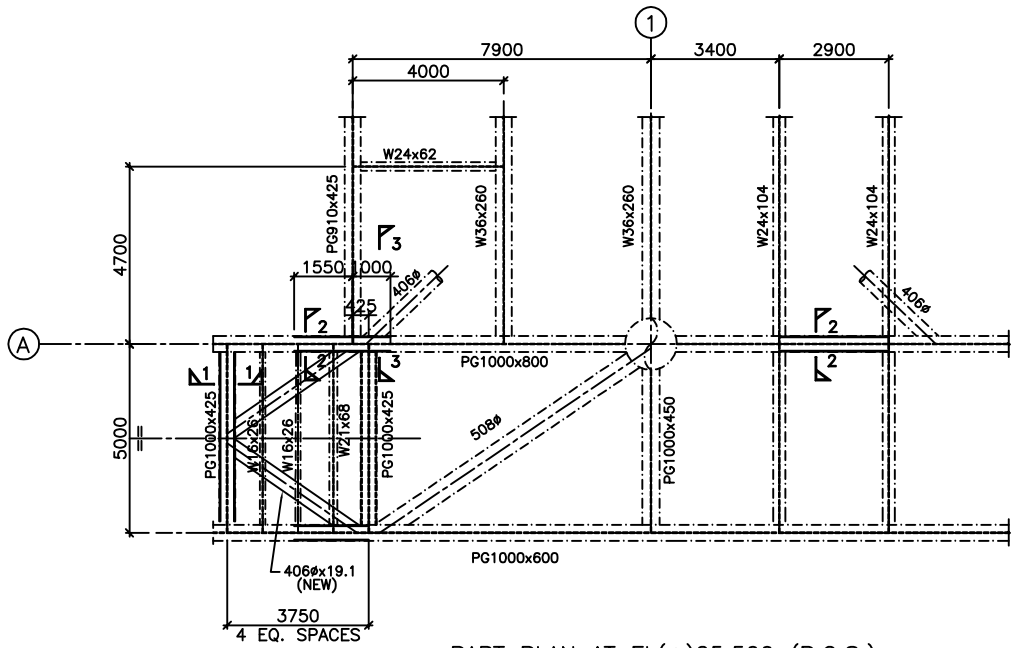


PART PLAN AT EL(+)25.500 (B.O.S.)

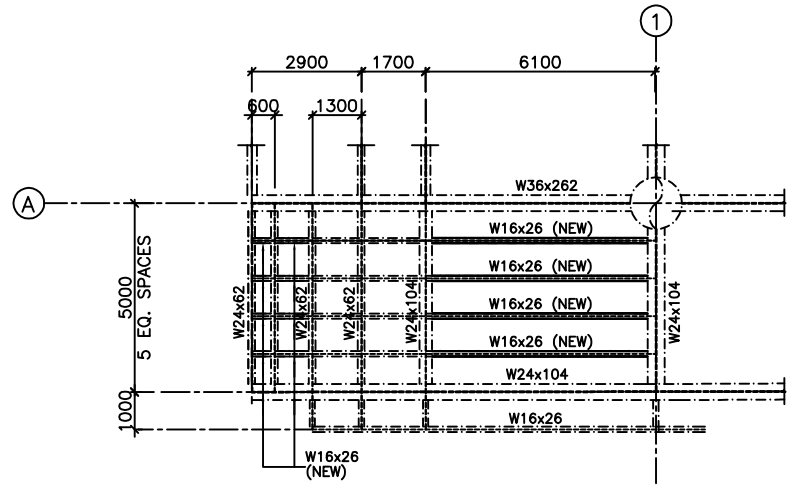


PART PLAN AT EL(+)18.100 (B.O.S.)

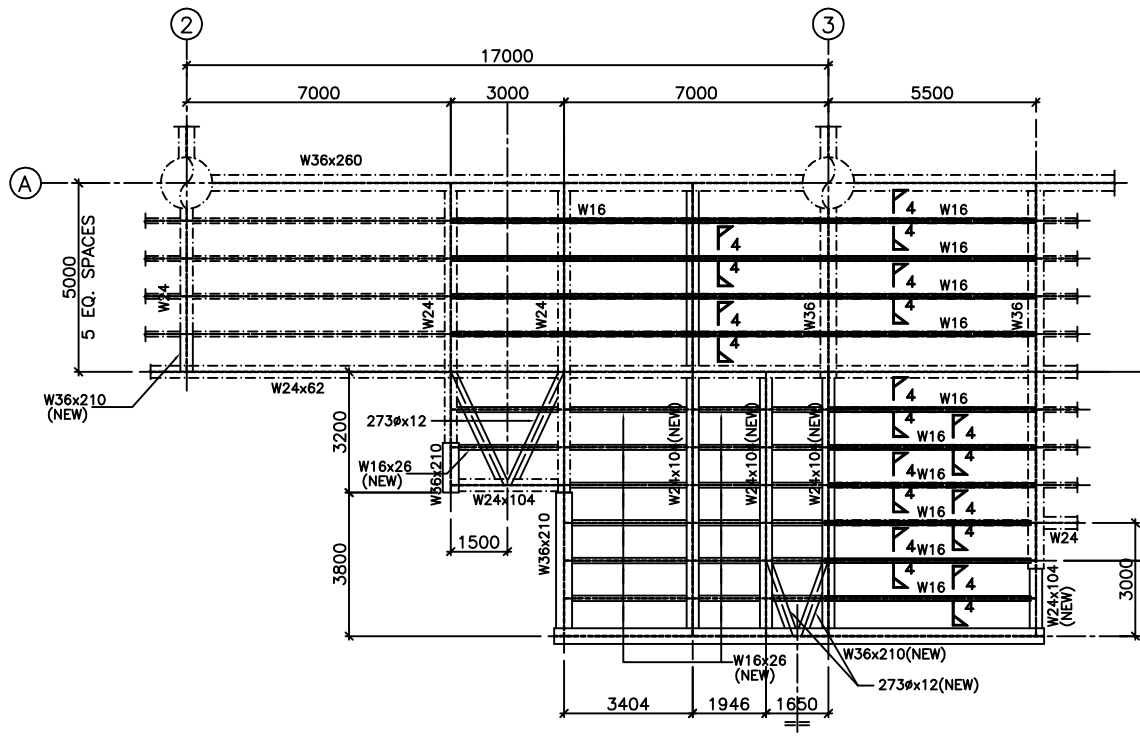

PART PLAN AT EL(+)18.100 (T.O.S.)

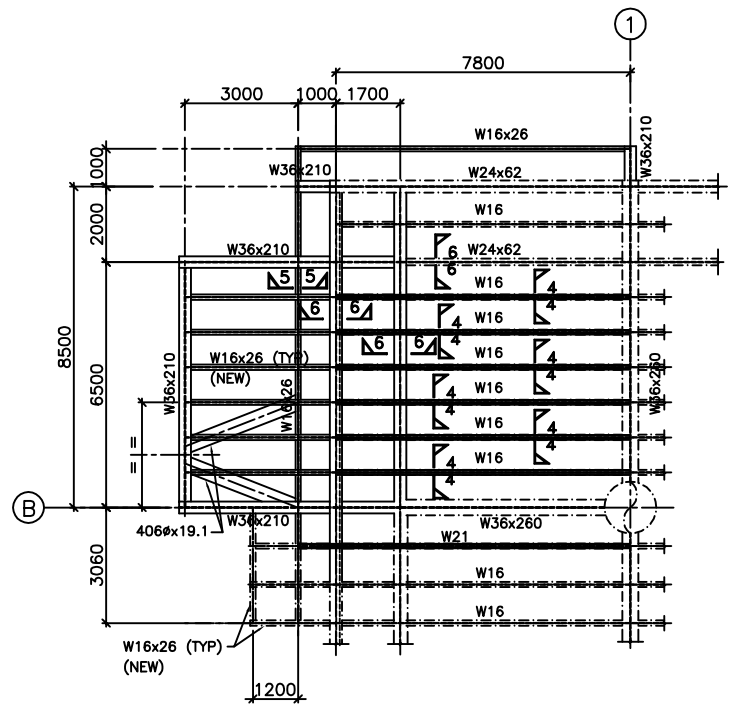

7800
3000
1000
1700
W16x26
W36x210
W24x62
W36x210
W16
W24x62
2000
W16
W16
W16

B774-103-83-43-0001

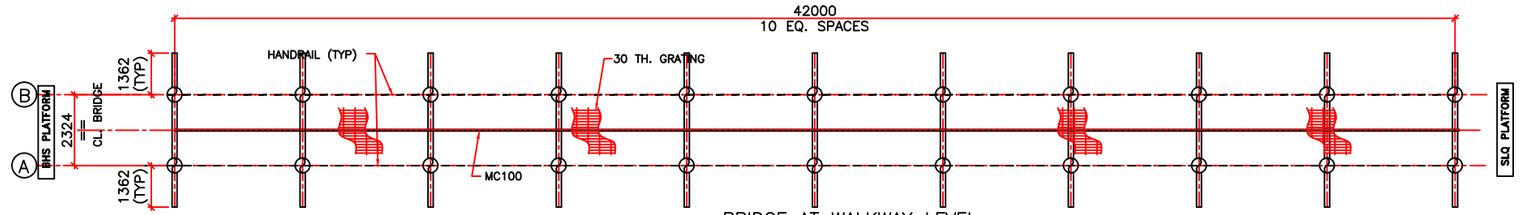


BRIDGE AT WALKWAY LEVEL

ALL MEMBERS ARE MB600 (U.N.O.)

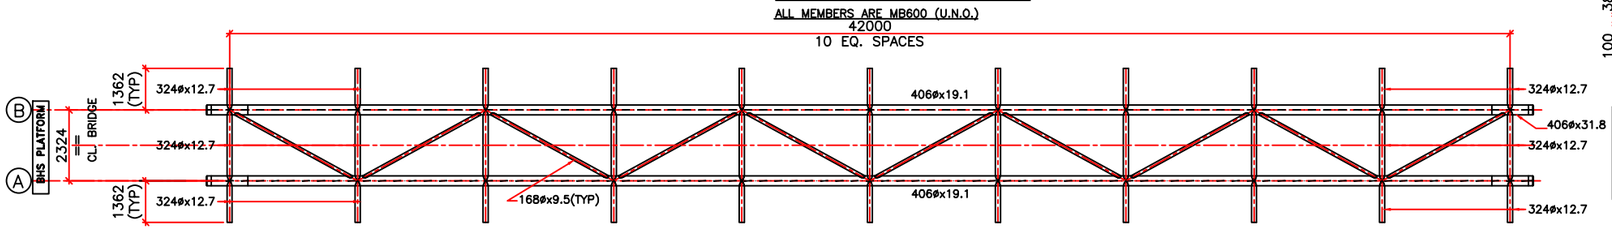


BRIDGE AT TOP CHORD

ALL MEMBERS ARE 273ø x12.7 (U.N.O.)

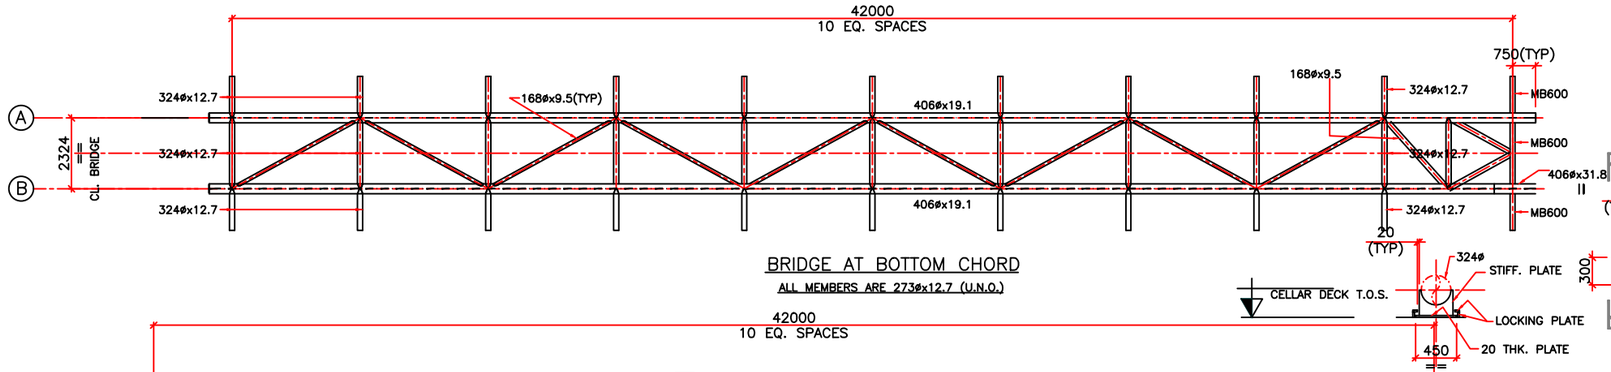


BRIDGE AT BOTTOM CHORD

ALL MEMBERS ARE 273ø x12.7 (U.N.O.)

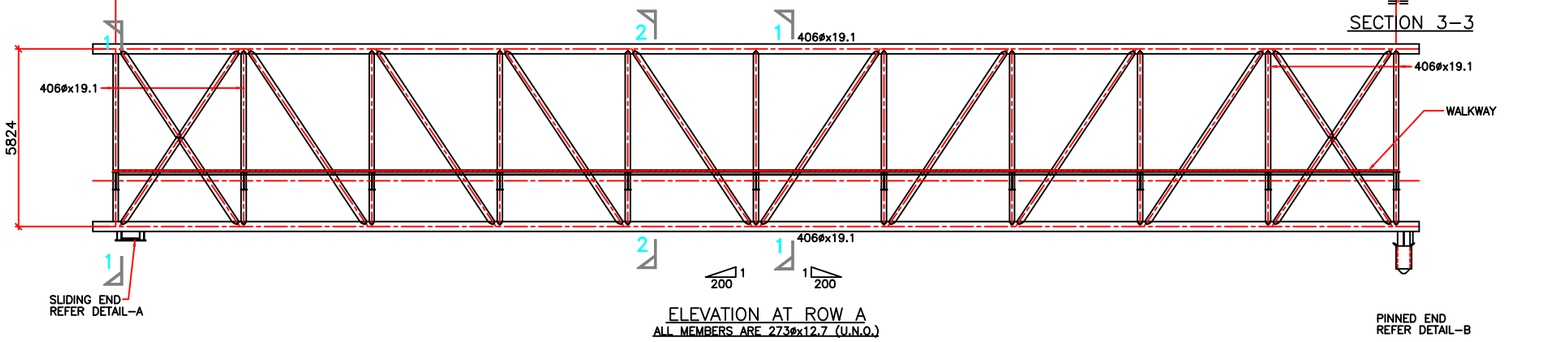


ELEVATION AT ROW A

ALL MEMBERS ARE 273ø x12.7 (U.N.O.)

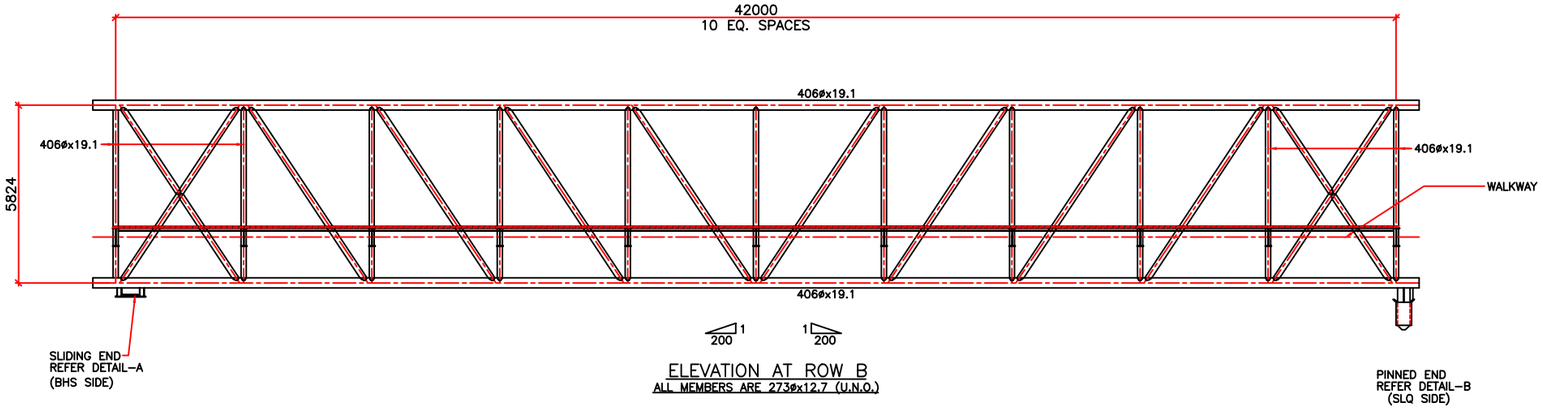


ELEVATION AT ROW B

ALL MEMBERS ARE 273ø x12.7 (U.N.O.)

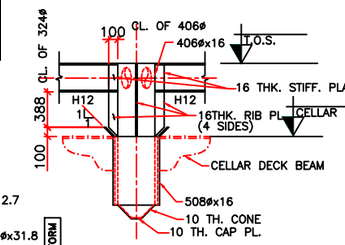


SECTION 4–4

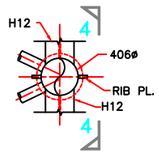


DETAIL–B

SECTION 3–3

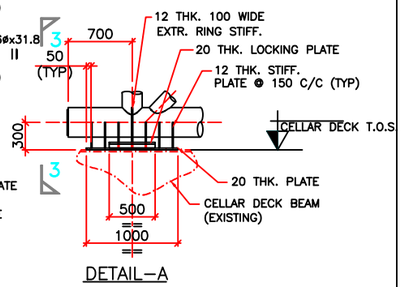

DETAIL–A

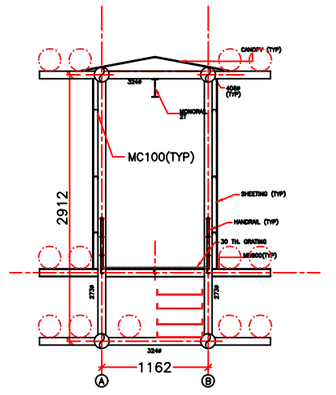

SECTION 1–1

SECTION 2–2

REF. DWG. NO.	REFERENCE DRAWING TITLE

NOTES :-

1. DO NOT SCALE THE DRAWING, WORK TO DIMENSIONS ONLY.
2. ALL DIMENSIONS ARE IN MM AND LEVELS ARE IN M U.N.O.
3. ALL ELEVATIONS ARE W.R.T. CHART DATUM (CD) 0.0M CHART DATUM FOR INDIAN WATERS SHALL BE 2.5M BELOW MEAN SEA LEVEL (MSL).
4. MATERIAL SPECIFICATIONS
   a) ALL STIFFENERS, FLANGE EXTENSION PLATES ETC. SHALL BE OF SAME / HIGHER GRADE AS ELEMENT TO WHICH THEY ARE CONNECTED U.N.O.
5. MATERIAL TYPES LISTED IN SC NOS SHALL CONFORM TO ONGC SPEC 6001 F.
6. FABRICATOR TO ENSURE MIN 75MM CLEAR GAP B/W HE WELDS FOR CROSS BRACES AND CROSS JOINTS.
7. ALL WELDS SHALL BE FULL PENETRATION WELDS.
8. FOR GRATING REFER EIL STD. 7–60–0802.
9. FOR HANDRAIL REFER EIL STD. 7–60–0801.

* ALL DETAILS, DIMENSIONS, LEVELS & MEMBER SIZES IN THE DRAWING ARE INDICATIVE AND ARE PROVIDED FOR BIDDERS UNDERSTANDING OF SCOPE OF WORK ONLY.ALL DETAILS SHOWN IN THE DRAWING SHALL BE VERIFIED BY CONTRACTOR DURING PRE–ENGINEERING SURVEY & DETAIL ENGINEERING SHALL BE CARRIED OUT BY CONTRACTOR FOR EXECUTION OF WORKS.

* ALL THE DIMENSIONS ARE IN MM AND LEVELS ARE IN METER (U.N.O.)

FOR TENDER PURPOSE ONLY

REV.	DATE	REVISIONS	BY	CHKD	APPD	PEM/PC
0	10.08.25	ISSUED FOR BIDS	MUNISH	AR	DP	

इंजीनियर्स इंडिया लिमिटेड ENGINEERS INDIA LIMITED (A Govt. of India Undertaking)

ऑयल एण्ड नेचुरल गैस कारपोरेशन लिमिटेड
OIL AND NATURAL GAS CORPORATION LIMITED

एम एच संपर्कता की मौजूदा पुल का नवीकरण/बदलाव	REFURBISHMENT/REPLACEMENT OF EXISTING BRIDGE AT MH ASSET
आई सी डबलू से आई सी जी के निचली छत पुल का सामान्य विन्यास एवं व्यौरा	G.A. AND DETAILS OF BHS TO SLQ LOWER DECK BRIDGE


SCALE	JOB NO.	UNIT	DIVN.	DEPT.	DWG. NO.	REV.
	B774	103	83	43	00001	A

3-1641-0501 REV.2 A1-841x594


प्रस्तुत आरेख एवं इसमें निहित डिज़ाइन इंजीनियर्स इंडिया लिमिटेड की संपत्ति है। ये मात्र उधार दिए गए हैं और उधारकर्ता ने यह स्पष्ट समझौता किया है कि न तो इन्हें पुनः मुद्रित किया जाएगा, न नकल की जाएगी, न उधार दिए जाएंगे, न प्रदर्शित किए जाएंगे और न ही सार्वजनिक और निजी प्रयोग के अलावा इनका कोई अन्य प्रयोग होगा और यह प्रयोग उधार देने वाले द्वारा उधारकर्ता को लिखित रूप में दी गई सहमति से होगा।

The drawing, design and details given on this format are the property of ENGINEERS INDIA LIMITED. They are merely loaned on the borrower's express agreement that they will not be reproduced, copied, exhibited or used, except in the limited way permitted by a written consent given by the lender to the borrower for the intended use.


B774-103-83-43-0002

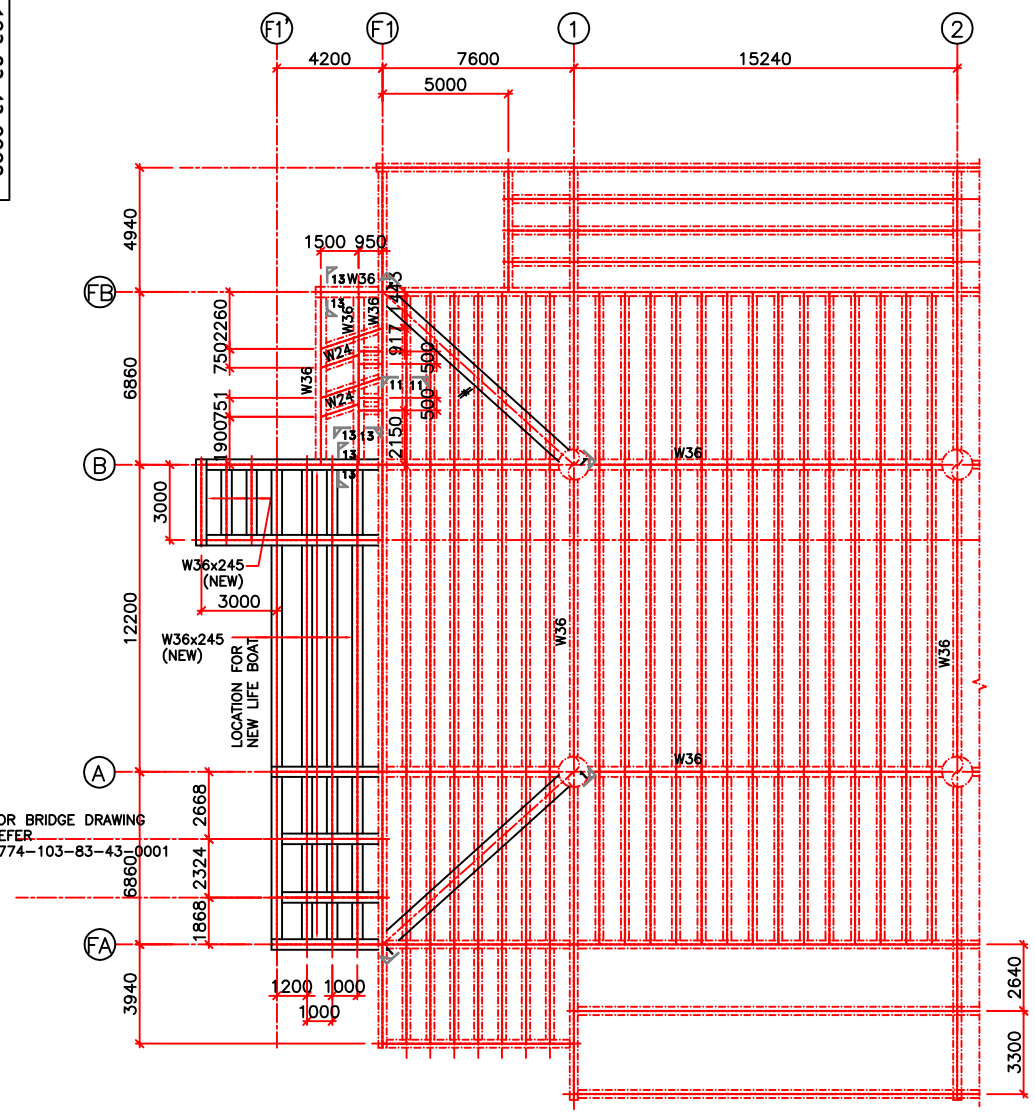

PART PLAN OF CELLAR DECK EL(+)18.288(T.O.S.)
(ALL MEMBERS ARE W24 (U.N.O.)

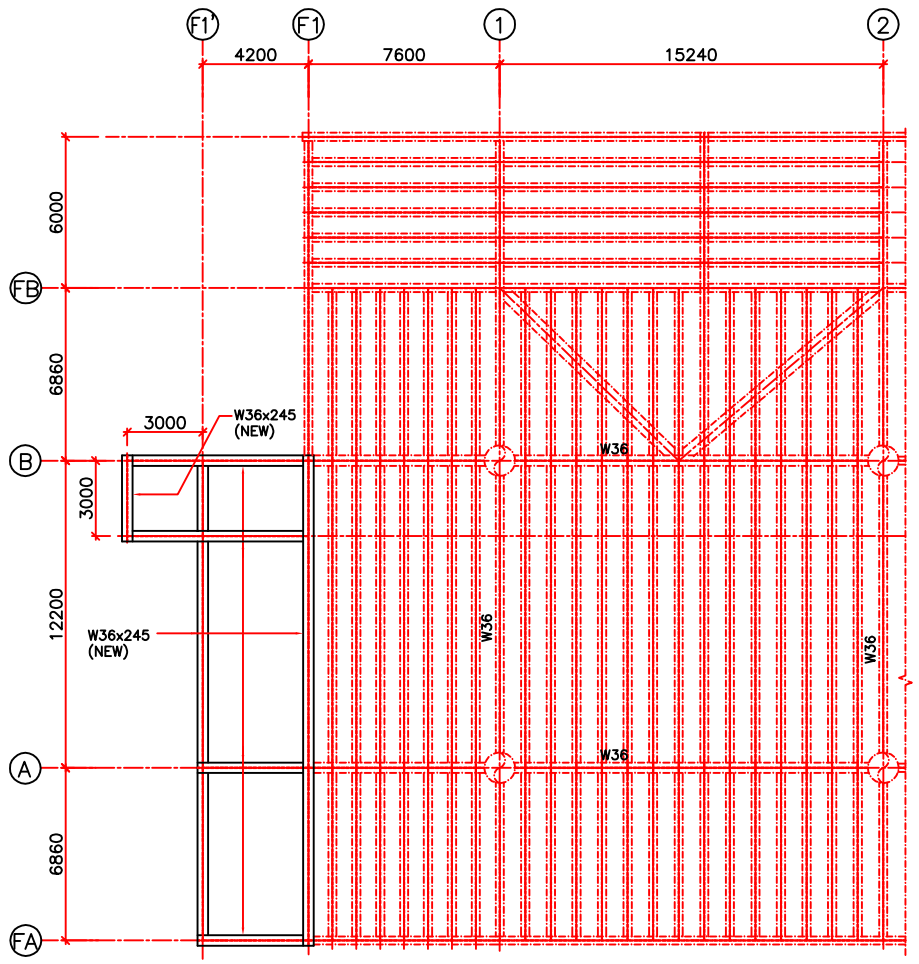

PART PLAN OF MAIN DECK EL(+)25.292(T.O.S.)
(ALL MEMBERS ARE W24 (U.N.O.)

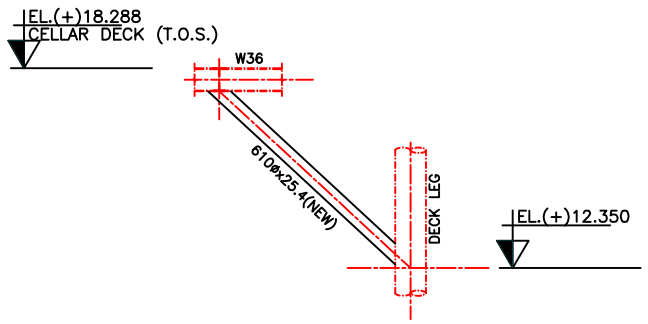

VIEW 1–1

REF. DWG. NO.	REFERENCE DRAWING TITLE

NOTES :-

1. DO NOT SCALE THE DRAWING, WORK TO DIMENSIONS ONLY.
2. ALL DIMENSIONS ARE IN MM AND LEVELS ARE IN M U.N.O.
3. ALL ELEVATIONS ARE W.R.T. CHART DATUM (CD) 0.0M CHART DATUM FOR INDIAN WATERS SHALL BE 2.5M BELOW MEAN SEA LEVEL (MSL).
4. MATERIAL SPECIFICATIONS
   a) ALL STIFFENERS, FLANGE EXTENSION PLATES ETC. SHALL BE OF SAME / HIGHER GRADE AS ELEMENT TO WHICH THEY ARE CONNECTED U.N.O.
5. MATERIAL TYPES LISTED IN SC NOS SHALL CONFORM TO ONGC SPEC 6001 F.
6. FABRICATOR TO ENSURE MIN 75MM CLEAR GAP B/W HE WELDS FOR CROSS BRACES AND CROSS JOINTS.
7. ALL WELDS SHALL BE FULL PENETRATION WELDS.
8. FOR GRATING REFER EIL STD. 7–60–0802.
9. FOR HANDRAIL REFER EIL STD. 7–60–0801.

* ALL DETAILS, DIMENSIONS, LEVELS & MEMBER SIZES IN THE DRAWING ARE INDICATIVE AND ARE PROVIDED FOR BIDDERS UNDERSTANDING OF SCOPE OF WORK ONLY.ALL DETAILS SHOWN IN THE DRAWING SHALL BE VERIFIED BY CONTRACTOR DURING PRE–ENGINEERING SURVEY & DETAIL ENGINEERING SHALL BE CARRIED OUT BY CONTRACTOR FOR EXECUTION OF WORKS.
* ALL THE DIMENSIONS ARE IN MM AND LEVELS ARE IN METER (U.N.O.)

FIELD NOTES

THE MEMBER MARKED SHALL BE ADJUSTED BY AVOIDING THE FOULING WITH EXISTING WALKWAY AS PER SITE DETAILS DURING DETAILED ENGINEERING.
* SINCE DRAWINGS OF BHS PLATFORM ARE NOT AVAILABLE, THE 3D MODEL AND NDT RESULTS ARE CONSIDERED FOR SIZING. THE MEMBER SIZE AND THICKNESS SHALL BE VERIFIED DURING DETAILED ENGINEERING FOR ALL MEMBERS BEFORE FINALIZING THE MODIFICATIONS.

ISSUED FOR TENDER

REV.	DATE	REVISIONS	BY	CHKD	APPD	PEM/PC
A	23.01.26	ISSUED FOR TENDER	MUNISH	AP	DP	

इंजीनियर्स इंडिया लिमिटेड ENGINEERS INDIA LIMITED (A Govt. of India Undertaking)

ऑयल एण्ड नेचुरल गैस कारपोरेशन लिमिटेड
OIL AND NATURAL GAS CORPORATION LIMITED

REFURBISHMENT/REPLACEMENT OF BRIDGES IN MH ASSET

MODIFICATION OF BHS DECK

SCALE	JOB NO.	UNIT	DIVN.	DEPT.	DWG. NO.	REV.
1:150	B774	103	83	43	0002	A

प्रस्तुत आरेख एवं इसमे निहित डिज़ाइन इंजीनियर्स इंडिया लिमिटेड की संपत्ति है और उसकी सुरक्षा किया है कि न तो इसे मुफ़्त: पुनरित किया जाएगा, न नकल की जाएगी, न उधार दिए जाएंगे, न प्रदर्शित किए जाएंगे और न ही सीमित और किसी प्रयोग के अलावा इसका कोई अन्य प्रयोग होगा और यह प्रयोग उधार देने वाले द्वारा उधारकर्ता को लिखित रूप में दी गई सहमति से होगा ।
The drawing, design and details given on this format are the property of ENGINEERS INDIA LIMITED. They are merely loaned on the borrower's express agreement that they will not be reproduced, copied, exhibited or used, except in the limited way permitted by a written consent given by the lender to the borrower for the intended use.

3-1641-0501 REV.2 A1-841x594

यह दस्तावेज़ एवं इसमें निहित डिज़ाइन डिस्क्लोज़र इंजीनियर्स इंडिया लिमिटेड की संपत्ति है और उसकी लिखित सहमति के बिना इसका पुनरुत्पादन, न प्रकाशित किया जाएगा, न प्रदर्शित किया जाएगा और न ही संलिखित और किसी प्रयोग के अलावा इसका कोई अन्य प्रयोग होगा और यह प्रयोग उधार देने वाले द्वारा उधारकर्ता को लिखित रूप से दी गई सहमति से होगा ।
The drawing, design and details given on this format are the property of ENGINEERS INDIA LIMITED. They are merely loaned on the borrower's express agreement that they will not be reproduced, copied, exhibited or used, except in the limited way permitted by a written consent given by the lender to the borrower for the intended use.

B774-103-83-43-0003

PART ELEVATION OF DECK ROW A

PART ELEVATION OF DECK ROW B

PART ELEVATION OF DECK ROW 1

PART ELEVATION OF DECK ROW 2

PART ELEVATION OF DECK ROW FA

PART ELEVATION OF DECK ROW FB

PART ELEVATION OF DECK ROW F1

PART ELEVATION OF DECK ROW F1'

SECTION 1–1

SECTION 2–2

SECTION 3–3

SECTION 4–4

SECTION 5–5

SECTION 6–6

SECTION 7–7

SECTION 8–8

SECTION 9–9

SECTION 10–10

SECTION 11–11

SECTION 12–12

SECTION 13–13

REF. DWG. NO.	REFERENCE DRAWING TITLE

NOTES :-

1. DO NOT SCALE THE DRAWING, WORK TO DIMENSIONS ONLY.
2. ALL DIMENSIONS ARE IN MM AND LEVELS ARE IN M U.N.O.
3. ALL ELEVATIONS ARE W.R.T. CHART DATUM (CD) 0.0M CHART DATUM FOR INDIAN WATERS SHALL BE 2.5M BELOW MEAN SEA LEVEL (MSL).
4. MATERIAL SPECIFICATIONS
   a) ALL STIFFENERS, FLANGE EXTENSION PLATES ETC. SHALL BE OF SAME / HIGHER GRADE AS ELEMENT TO WHICH THEY ARE CONNECTED U.N.O.
5. MATERIAL TYPES LISTED IN SC NOS SHALL CONFORM TO ONGC SPEC 6001 F.
6. FABRICATOR TO ENSURE MIN 75MM CLEAR GAP B/W HE WELDS FOR CROSS BRACES AND CROSS JOINTS.
7. ALL WELDS SHALL BE FULL PENETRATION WELDS.
8. FOR GRATING REFER EIL STD. 7–60–0802.
9. FOR HANDRAIL REFER EIL STD. 7–60–0801.

* ALL DETAILS, DIMENSIONS, LEVELS & MEMBER SIZES IN THE DRAWING ARE INDICATIVE AND ARE PROVIDED FOR BIDDERS UNDERSTANDING OF SCOPE OF WORK ONLY.ALL DETAILS SHOWN IN THE DRAWING SHALL BE VERIFIED BY CONTRACTOR DURING PRE–ENGINEERING SURVEY & DETAIL ENGINEERING SHALL BE CARRIED OUT BY CONTRACTOR FOR EXECUTION OF WORKS.
* ALL THE DIMENSIONS ARE IN MM AND LEVELS ARE IN METER (U.N.O.)

FIELD NOTES

\# THE MEMBER MARKED SHALL BE ADJUSTED BY AVOIDING THE FOULING WITH EXISTING WALKWAY AS PER SITE DETAILS DURING DETAILED ENGINEERING.
* SINCE DRAWINGS OF BHS PLATFORM ARE NOT AVAILABLE, THE 3D MODEL AND NDT RESULTS ARE CONSIDERED FOR SIZING. THE MEMBER SIZE AND THICKNESS SHALL BE VERIFIED DURING DETAILED ENGINEERING FOR ALL MEMBERS BEFORE FINALIZING THE MODIFICATIONS.

ISSUED FOR TENDER

REV.	DATE	REVISIONS	BY	CHKD	APPD	PEM/PC
A	23.01.26	ISSUED FOR TENDER	MUNISH	AP	DP	

इंजीनियर्स इंडिया लिमिटेड ENGINEERS INDIA LIMITED (A Govt. of India Undertaking)

ऑयल एण्ड नेचुरल गैस कारपोरेशन लिमिटेड
OIL AND NATURAL GAS CORPORATION LIMITED


REFURBISHMENT/REPLACEMENT OF BRIDGES IN MH ASSET

MODIFICATION OF BHS DECK


SCALE	JOB NO.	UNIT	DIVN.	DEPT.	DWG. NO.	REV.
1:150	B774	103	83	43	0003	A

3-1641-0501 REV.2 A1-841x594

B774-103-83-43-0004

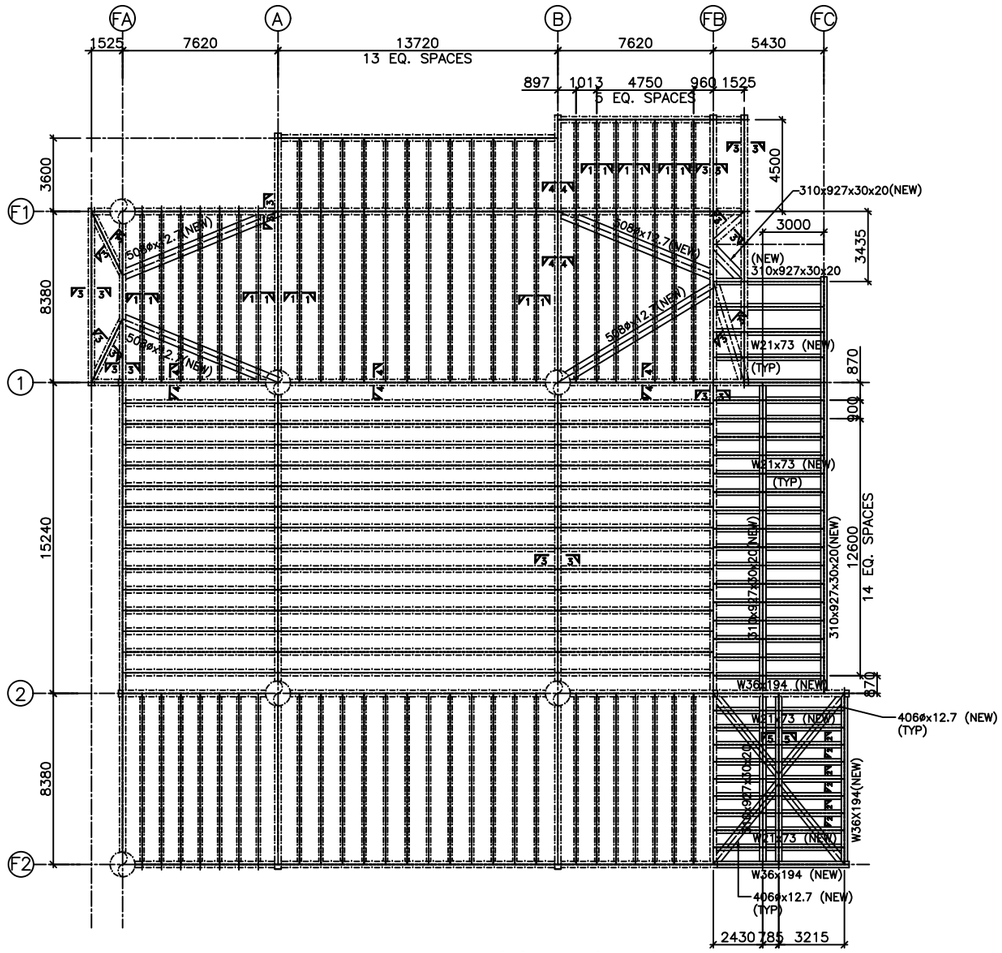

PART PLAN OF LOWER DECK EL(+)18.288(T.O.S.)

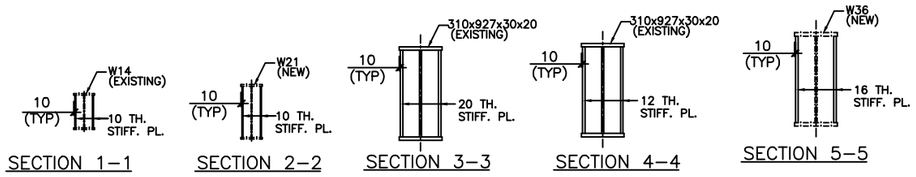

SECTION 1–1 SECTION 2–2 SECTION 3–3 SECTION 4–4 SECTION 5–5

REF. DWG. NO.	REFERENCE DRAWING TITLE
HTFC1-8-401-2101	LOWER DECK FRAMING PLAN (SLQ)
HTFC1-8-402-2102	LOWER DECK PLATING PLAN (SLQ)
HTFC1-8-403-2201	UPPER DECK FRAMING PLAN (SLQ)
HTFC1-8-404-2202	UPPER DECK BEAM PLAN (SLQ)
HTFC1-8-421-2401	TRUSS ELEVATION ROW 1&2 (SLQ)
HTFC1-8-404-2402	TRUSS ELEVATION ROW A&B (SLQ)

NOTES :-

1. DO NOT SCALE THE DRAWING, WORK TO DIMENSIONS ONLY.
2. ALL DIMENSIONS ARE IN MM AND LEVELS ARE IN M U.N.O.
3. ALL ELEVATIONS ARE W.R.T. CHART DATUM (CD) 0.0M CHART DATUM FOR INDIAN WATERS SHALL BE 2.5M BELOW MEAN SEA LEVEL (MSL).
4. MATERIAL SPECIFICATIONS
   a) ALL STIFFENERS, FLANGE EXTENSION PLATES ETC. SHALL BE OF SAME / HIGHER GRADE AS ELEMENT TO WHICH THEY ARE CONNECTED U.N.O.
5. MATERIAL TYPES LISTED IN SC NOS SHALL CONFORM TO ONGC SPEC 6001 F.
6. FABRICATOR TO ENSURE MIN 75MM CLEAR GAP B/W HE WELDS FOR CROSS BRACES AND CROSS JOINTS.
7. ALL WELDS SHALL BE FULL PENETRATION WELDS.
8. FOR GRATING REFER EIL STD. 7-60-0802.
9. FOR HANDRAIL REFER EIL STD. 7-60-0801.
10. THE MATERIAL AND AVAILABILITY OF INTERNAL STIFFENERS FOR LEG & CONE SHALL BE CHECKED DURING DETAILED ENGINEERING STAGE & ACCORDINGLY DESIGN SHALL BE UPDATED.

- ALL DETAILS, DIMENSIONS, LEVELS & MEMBER SIZES IN THE DRAWING ARE INDICATIVE AND ARE PROVIDED FOR BIDDERS UNDERSTANDING OF SCOPE OF WORK ONLY.ALL DETAILS SHOWN IN THE DRAWING SHALL BE VERIFIED BY CONTRACTOR DURING PRE-ENGINEERING SURVEY & DETAIL ENGINEERING SHALL BE CARRIED OUT BY CONTRACTOR FOR EXECUTION OF WORKS.
- ALL THE DIMENSIONS ARE IN MM AND LEVELS ARE IN METER (U.N.O.)

ISSUED FOR TENDER

REV.	DATE	REVISIONS	BY	CHKD	APPD	PEM/PC
0	29.01.26	ISSUED FOR TENDER	MUNISH	AMS	DP	

इंजीनियर्स इंडिया लिमिटेड ENGINEERS INDIA LIMITED (A Govt. of India Undertaking)

ऑयल एण्ड नेचुरल गैस कारपोरेशन लिमिटेड
OIL AND NATURAL GAS CORPORATION LIMITED

REFURBISHMENT/REPLACEMENT OF BRIDGES IN MH ASSET


STRENGTHENING OF SLQ DECK

SCALE	JOB NO.	UNIT	DIVN.	DEPT.	DWG. NO.	REV.
1:150	B774	103	83	43	0004	0


प्रस्तुत आरेख एवं इसमें निहित डिजाइन इंजीनियर्स इंडिया लिमिटेड को संपत्ति है। ये मात्र उधार दिए गए है और उपकर्ता ने यह स्पष्ट समझौता किया है कि न तो इन्हें पुनः मुद्रित किया जाएगा, न नकल की जाएगी, न उधार दिए जाएंगे, न पुनर्निर्गत किए जाएंगे और न ही संलिप्त और किसी प्रयोग के अलावा इनका कोई अन्य प्रयोग होगा और यह प्रयोग उधार देने वाले द्वारा उपकर्ता को लिखित रूप में दी गई सहमति से होगा ।

The drawing, design and details given on this format are the property of ENGINEERS INDIA LIMITED. They are merely loaned on the borrower's express agreement that they will not be reproduced, copied, exhibited or used, except in the limited way permitted by a written consent given by the lender to the borrower for the intended use.


B774-103-83-43-0005

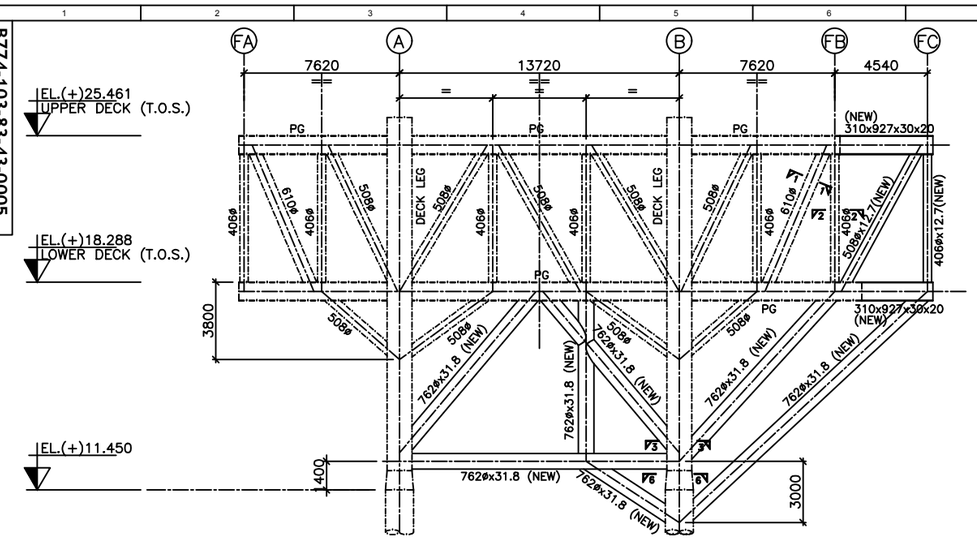


ELEVATION OF DECK ROW 1

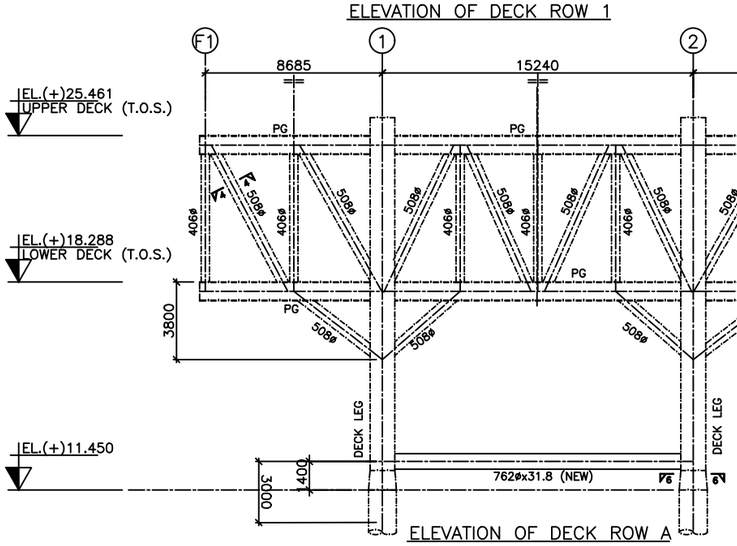


ELEVATION OF DECK ROW A

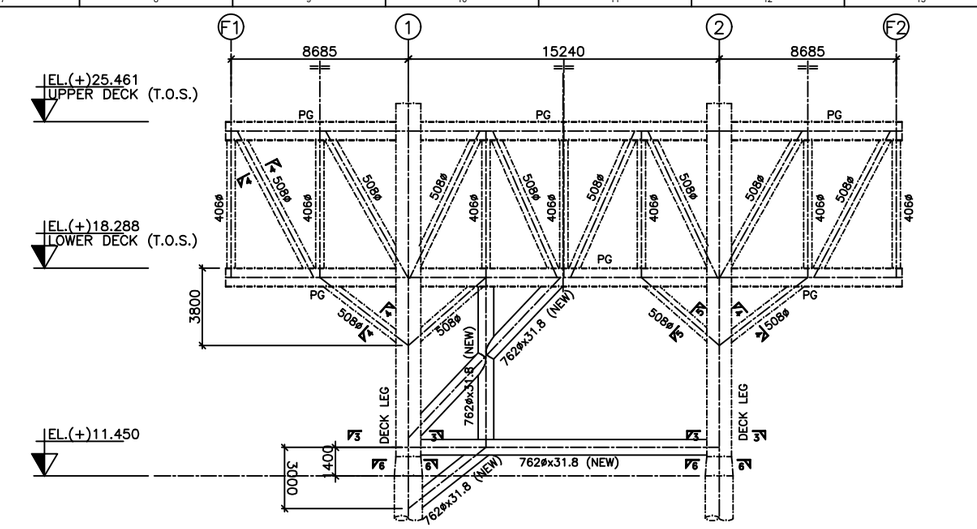


ELEVATION OF DECK ROW B

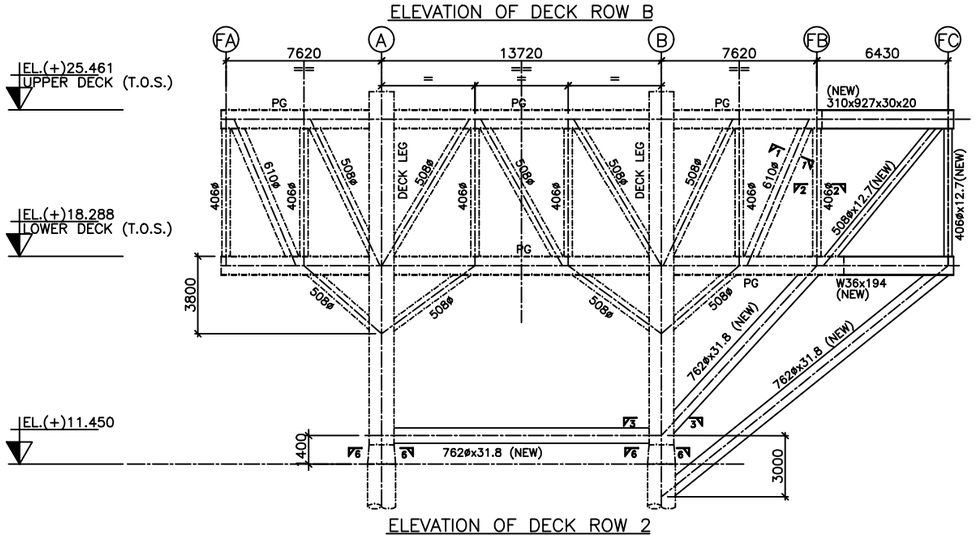


ELEVATION OF DECK ROW 2

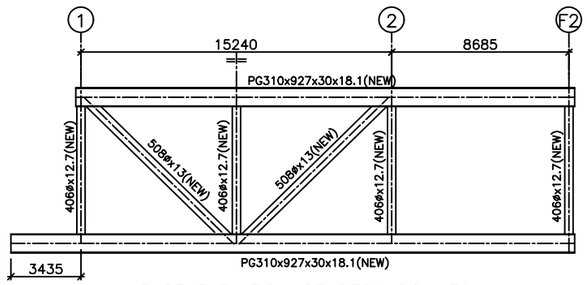


PART ELEVATION OF DECK ROW FC

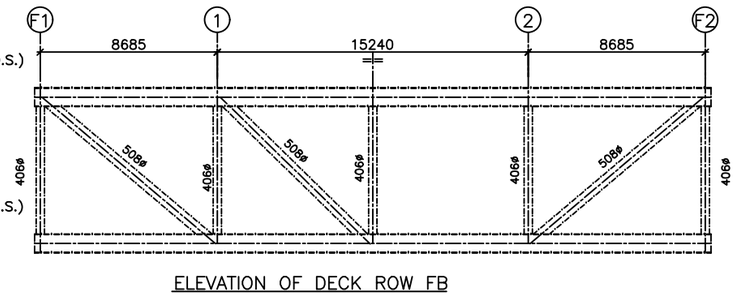


ELEVATION OF DECK ROW FB

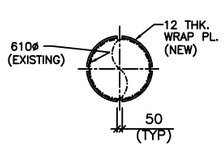


SECTION 1–1

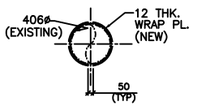


SECTION 2–2

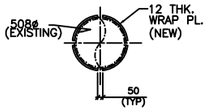


SECTION 4–4

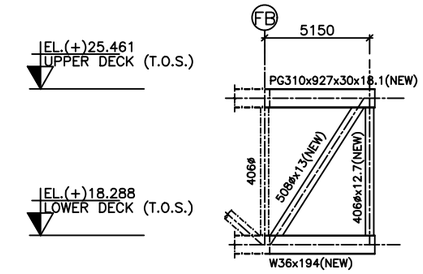


PART ELEVATION OF DECK ROW F2

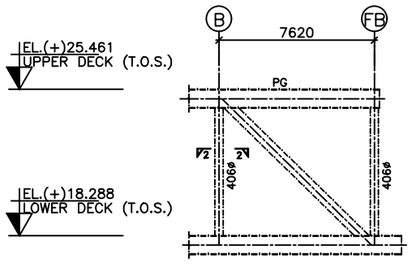


PART ELEVATION OF DECK ROW F1

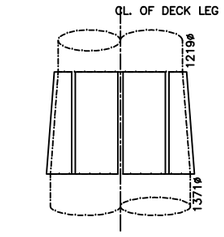


VIEW A–A
STRENGTHENING STABBING
POINT AT ROW B

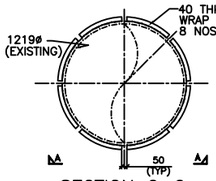

SECTION 6–6

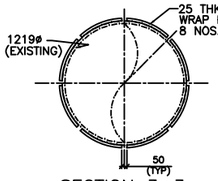

SECTION 3–3

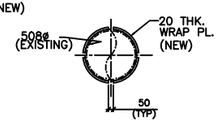

SECTION 5–5

REF. DWG. NO.	REFERENCE DRAWING TITLE
HTFC1-8-401-2101	LOWER DECK FRAMING PLAN (SLQ)
HTFC1-8-402-2102	LOWER DECK PLATING PLAN (SLQ)
HTFC1-8-403-2201	UPPER DECK FRAMING PLAN (SLQ)
HTFC1-8-404-2202	UPPER DECK BEAM PLAN (SLQ)
HTFC1-8-421-2401	TRUSS ELEVATION ROW 1&2 (SLQ)
HTFC1-8-404-2202	TRUSS ELEVATION ROW A&B (SLQ)

NOTES :-

1. DO NOT SCALE THE DRAWING, WORK TO DIMENSIONS ONLY.
2. ALL DIMENSIONS ARE IN MM AND LEVELS ARE IN M U.N.O.
3. ALL ELEVATIONS ARE W.R.T. CHART DATUM (CD) 0.0M CHART DATUM FOR INDIAN WATERS SHALL BE 2.5M BELOW MEAN SEA LEVEL (MSL).
4. MATERIAL SPECIFICATIONS
   a) ALL STIFFENERS, FLANGE EXTENSION PLATES ETC. SHALL BE OF SAME / HIGHER GRADE AS ELEMENT TO WHICH THEY ARE CONNECTED U.N.O.
5. MATERIAL TYPES LISTED IN SC NOS SHALL CONFORM TO ONGC SPEC 6001 F.
6. FABRICATOR TO ENSURE MIN 75MM CLEAR GAP B/W HE WELDS FOR CROSS BRACES AND CROSS JOINTS.
7. ALL WELDS SHALL BE FULL PENETRATION WELDS.
8. FOR GRATING REFER EIL STD. 7–60–0802.
9. FOR HANDRAIL REFER EIL STD. 7–60–0801.
10. THE MATERIAL AND AVAILABILITY OF INTERNAL STIFFENERS FOR LEG & CONE SHALL BE CHECKED DURING DETAILED ENGINEERING STAGE & ACCORDINGLY DESIGN SHALL BE UPDATED.

* ALL DETAILS, DIMENSIONS, LEVELS & MEMBER SIZES IN THE DRAWING ARE INDICATIVE AND ARE PROVIDED FOR BIDDERS UNDERSTANDING OF SCOPE OF WORK ONLY.ALL DETAILS SHOWN IN THE DRAWING SHALL BE VERIFIED BY CONTRACTOR DURING PRE-ENGINEERING SURVEY & DETAIL ENGINEERING SHALL BE CARRIED OUT BY CONTRACTOR FOR EXECUTION OF WORKS.
* ALL THE DIMENSIONS ARE IN MM AND LEVELS ARE IN METER (U.N.O.)

ISSUED FOR TENDER

REV.	DATE	REVISIONS	BY	CHKD	APPD	PEM/PC
0	29.01.26	ISSUED FOR TENDER	MUNISH	AMS	DP	

इंजीनियर्स इंडिया लिमिटेड ENGINEERS INDIA LIMITED (A Govt. of India Undertaking)

ऑयल एण्ड नेचुरल गैस कारपोरेशन लिमिटेड
OIL AND NATURAL GAS CORPORATION LIMITED

REFURBISHMENT/REPLACEMENT OF BRIDGES IN MH ASSET


STRENGTHENING OF SLQ DECK

SCALE	JOB NO.	UNIT	DIVN.	DEPT.	DWG. NO.	REV.
1:150	B774	103	83	43	0005	0


3-1641-0501 REV.2 A1-841x594

प्रस्तुत आरेख एवं इसमें निहित डिज़ाइन इंजीनियर्स इंडिया लिमिटेड की संपत्ति है। ये मात्र उधार दिए गए हैं और उधारकर्ता ने यह स्पष्ट समझौता किया है कि न तो इन्हें पुनः मुद्रित किया जाएगा, न नकल की जाएगी, न उधार दिए जाएंगे, न पुनर्निर्मित किए जाएंगे और न ही संलिप्त और किसी प्रयोग के अलावा इनका कोई अन्य प्रयोग होगा और यह प्रयोग उधार देने वाले द्वारा उधारकर्ता को लिखित रूप में दी गई सहमति से होगा।
The property of ENGINEERS INDIA LIMITED. They are merely loaned on the borrower's express agreement that they will not be reproduced, copied, exhibited or used, except in the limited way permitted by a written consent given by the lender to the borrower for the intended use.

B774-103-83-43-0006

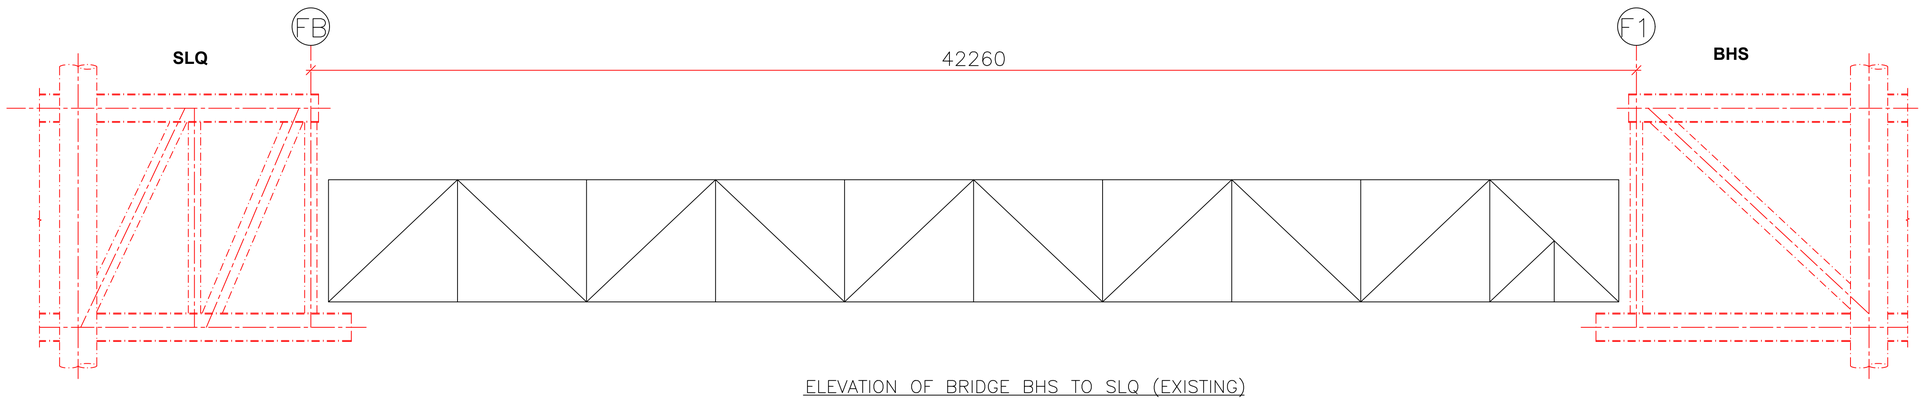

ELEVATION OF BRIDGE BHS TO SLQ (EXISTING)

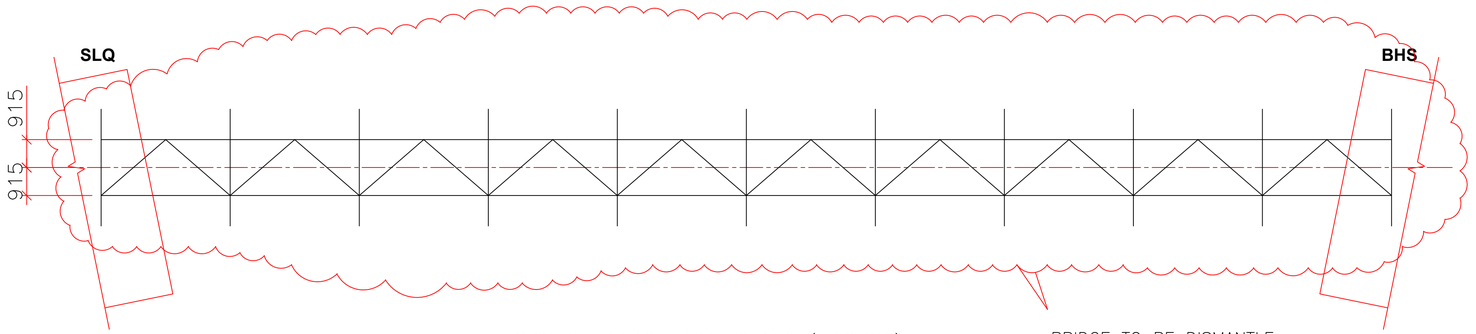

PLAN OF BRIDGE BHS TO SLQ (EXISTING)

BRIDGE TO BE DISMANTLE

REF. DWG. NO.	REFERENCE DRAWING TITLE

NOTES :-

1. DO NOT SCALE THE DRAWING, WORK TO DIMENSIONS ONLY.
2. ALL DIMENSIONS ARE IN MM AND LEVELS ARE IN M U.N.O.
3. THE EXISTING BHS–SLQ BRIDGE SHALL BE DISMANTLED AFTER ERECTION AND COMMISSIONING OF NEW BHS–SLQ BRIDGE ON THE SOUTH SIDE.
4. REQUIRED STRENGTHENING OF EXISTING BHS–SLQ BRIDGE SHALL BE DESIGNED DURING DETAILED ENGINEERING STAGE FOR DISMANTLING THE BRIDGE AS A WHOLE (PREFERABLE).
5. CONTRACTOR SHALL SUBMIT THE DETAILED DISMANTLING SCHEME DURING DETAILED ENGINEERING STAGE.

ISSUED FOR TENDER

REV.	DATE	REVISIONS	BY	CHKD	APPD	PEM/PC
0	10.10.25	ISSUED FOR TENDER	MUNISH	NS	DP	

इंजीनियर्स इंडिया लिमिटेड (भारत सरकार का उपक्रम) ENGINEERS INDIA LIMITED (A Govt. of India Undertaking)

ऑयल एण्ड नेचुरल गैस कारपोरेशन लिमिटेड
OIL AND NATURAL GAS CORPORATION LIMITED

REFURBISHMENT/REPLACEMENT OF BRIDGES IN MH ASSET

BHS SLQ BRIDGE (DISMANTLING)

SCALE	JOB NO.	UNIT	DIVN.	DEPT.	DWG. NO.	REV.
1:150	B774	103	83	43	0006	0

3-1641-0501 REV.2 A1-841x594

प्रस्तुत आरेख एवं इसमें निहित डिजाइन इंजीनियर्स इंडिया लिमिटेड की संपत्ति है। ये मात्र उधार दिए गए हैं और उधारकर्ता ने यह स्पष्ट समझौता किया है कि न तो इन्हें पुनः मुद्रित किया जाएगा, न नकल की जाएगी, न उधार दिए जाएंगे, न प्रदर्शित किए जाएंगे और न ही सहित और किसी प्रयोग के अलावा इनका कोई अन्य प्रयोग होगा और यह प्रयोग उधार देने वाले द्वारा उधारकर्ता को लिखित रूप से दी गई सहमति से होगा।

The drawing, design and details given on this format are the property of ENGINEERS INDIA LIMITED. They are merely loaned on the borrower's express agreement that they will not be reproduced, copied, exhibited or used, except in the limited way permitted by a written consent given by the lender to the borrower for the intended use.