
SHIVANSH / ONGC BRRP - SOURCE-INFORMED PRELIMINARY ARRANGEMENT

ICW - ICG LOWER DECK | SHV-BRRP-101-GA-P01 | Rev P1

STUDY REFERENCE ONLY - NOT FOR FABRICATION, PROCUREMENT, LIFTING OR INSTALLATION

Source model and cross-section reproduced from uploaded report; no new member sizing or structural verification performed.

A. SOURCE REPLACEMENT-STUDY MODEL

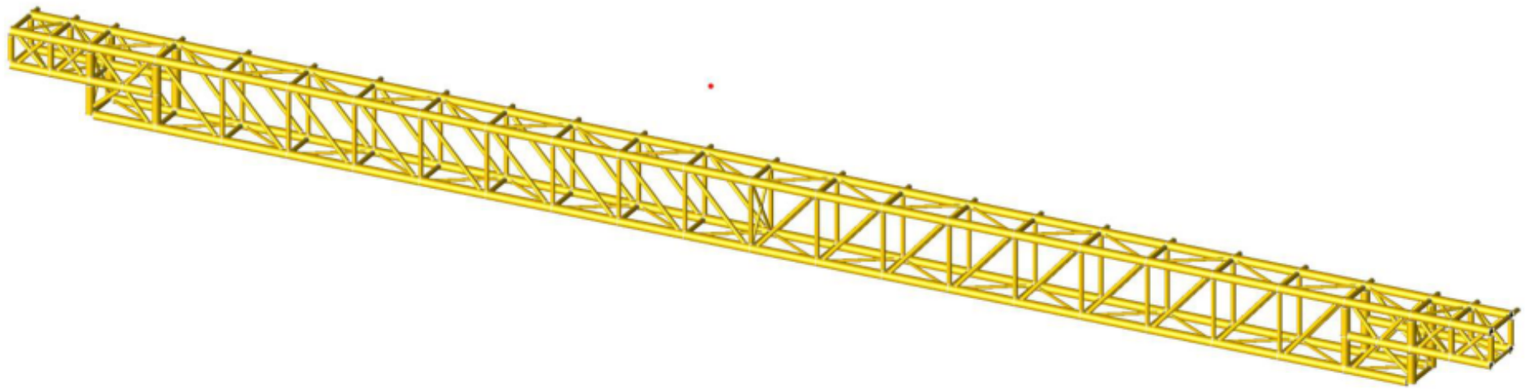

Source: B774-000-83-43-BPR-0004 Rev 0 | uploaded combined PDF p.133

B. SOURCE CROSS-SECTION



Overall width and structural depth: verify

Walkway loading width: 1.2 m (report basis)

C. LONGITUDINAL REFERENCE / SUPPORT INTERFACES - SCHEMATIC, NOT TO SCALE



Approximate 3D-model gap: 54.5 m | final bearing centres, skew, elevations, offsets and movement envelope require survey.

Landing reference: ICW: grid 4 northside; ICG: grid 3 southside; confirm against current survey and controlling drawings.

The reproduced model indicates braced space-truss framing. No panel spacing, section size or joint detail is adopted here.

D. DESIGN DEVELOPMENT NOTES

1. Retain report geometry only as a study reference; resolve actual support positions and dimensions before detailed design.
2. Report steel yield basis is 50 ksi; procurement grade, toughness, weldability and material requirements still require approval.
3. Report walkway loading is 250 kg/m2; validate loading, combinations, movements, serviceability and fatigue criteria.
4. Do not derive welds, bolt sizes, bearing travel, lifting points or plate thicknesses from model pictures or quantity totals.
5. Include permanent, temporary, lifting, transport and installation checks plus existing-platform/jacket capacity.
6. Incorporate applicable ICG/ICP jacket strengthening and landing modifications from SOW and structural addendum.

SOURCE: B774-000-83-43-BPR-0004 Rev 0; Report pp. 5-7 of 27; combined PDF pp.133-135 | 25 Oct 2026 | No AFC approval implied.


SHIVANSH / ONGC BRRP - SOURCE-INFORMED PRELIMINARY ARRANGEMENT

ICP - ICG LOWER DECK | SHV-BRRP-102-GA-P01 | Rev P1

STUDY REFERENCE ONLY - NOT FOR FABRICATION, PROCUREMENT, LIFTING OR INSTALLATION


Source model and cross-section reproduced from uploaded report; no new member sizing or structural verification performed.

A. SOURCE REPLACEMENT-STUDY MODEL

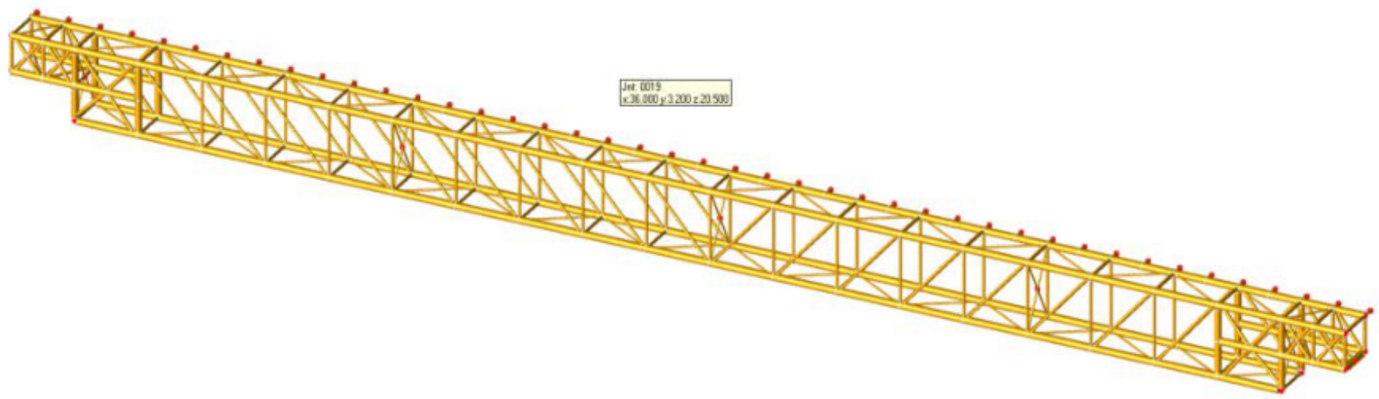

Source: B774-000-83-43-BPR-0003 Rev 0 | uploaded combined PDF p.197

B. SOURCE CROSS-SECTION

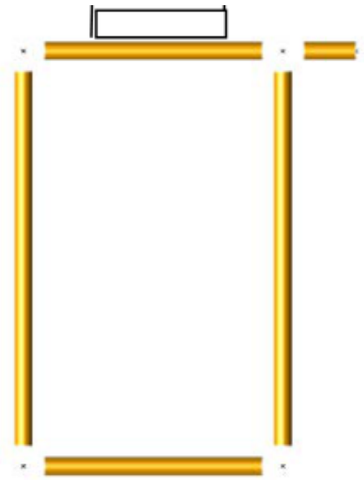

Overall width and structural depth: verify

Walkway loading width: 1.2 m (report basis)

C. LONGITUDINAL REFERENCE / SUPPORT INTERFACES - SCHEMATIC, NOT TO SCALE



Approximate 3D-model gap: 80.5 m | final bearing centres, skew, elevations, offsets and movement envelope require survey.

Landing reference: ICP: grid 3 northside; ICG: scramble-net area; confirm against current survey and controlling drawings.

The reproduced model indicates braced space-truss framing. No panel spacing, section size or joint detail is adopted here.

D. DESIGN DEVELOPMENT NOTES

1. Retain report geometry only as a study reference; resolve actual support positions and dimensions before detailed design.
2. Report steel yield basis is 50 ksi; procurement grade, toughness, weldability and material requirements still require approval.
3. Report walkway loading is 250 kg/m2; validate loading, combinations, movements, serviceability and fatigue criteria.
4. Do not derive welds, bolt sizes, bearing travel, lifting points or plate thicknesses from model pictures or quantity totals.
5. Include permanent, temporary, lifting, transport and installation checks plus existing-platform/jacket capacity.
6. Incorporate applicable ICG/ICP jacket strengthening and landing modifications from SOW and structural addendum.

SOURCE: B774-000-83-43-BPR-0003 Rev 0; Report pp. 5-8 of 20; combined PDF pp.196-199 | 25 Oct 2026 | No AFC approval implied.


SHIVANSH / ONGC BRRP - SOURCE-INFORMED PRELIMINARY ARRANGEMENT

BHS - SLQ LOWER DECK | SHV-BRRP-103-GA-P01 | Rev P1

STUDY REFERENCE ONLY - NOT FOR FABRICATION, PROCUREMENT, LIFTING OR INSTALLATION


Source model and cross-section reproduced from uploaded report; no new member sizing or structural verification performed.

A. SOURCE REPLACEMENT-STUDY MODEL

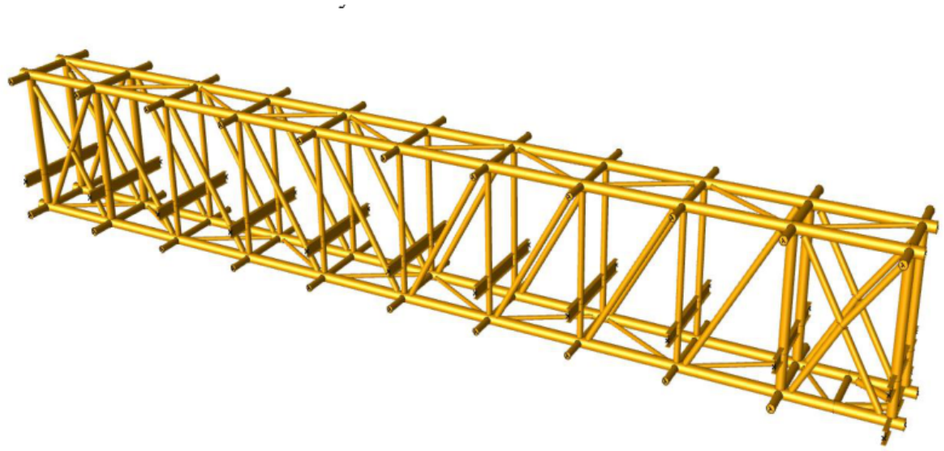

Source: B774-000-83-43-BPR-0005 Rev A | uploaded combined PDF p.98

B. SOURCE CROSS-SECTION

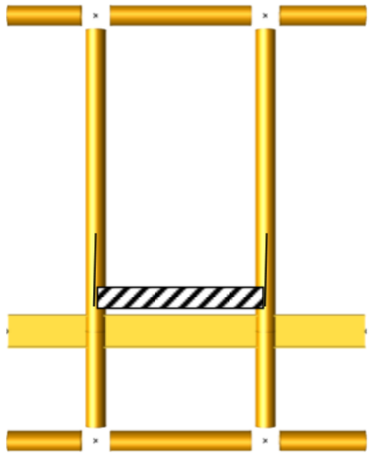

Overall width and structural depth: verify

Walkway loading width: 2.324 m (report basis)

C. LONGITUDINAL REFERENCE / SUPPORT INTERFACES - SCHEMATIC, NOT TO SCALE



Approximate 3D-model gap: 40 m | final bearing centres, skew, elevations, offsets and movement envelope require survey.

Landing reference: BHS: near A1 southside; SLQ: near B2 southside; confirm against current survey and controlling drawings.

The reproduced model indicates braced space-truss framing. No panel spacing, section size or joint detail is adopted here.

D. DESIGN DEVELOPMENT NOTES

1. Retain report geometry only as a study reference; resolve actual support positions and dimensions before detailed design.
2. Report steel yield basis is 50 ksi; procurement grade, toughness, weldability and material requirements still require approval.
3. Report walkway loading is 250 kg/m2; validate loading, combinations, movements, serviceability and fatigue criteria.
4. Do not derive welds, bolt sizes, bearing travel, lifting points or plate thicknesses from model pictures or quantity totals.
5. Include permanent, temporary, lifting, transport and installation checks plus existing-platform/jacket capacity.
6. SLQ fixed support is supported by the study; SOW 6.3.3(f) says sliding. Resolve this contradiction by technical query.

SOURCE: B774-000-83-43-BPR-0005 Rev A; Report pp. 5-8 of 36; combined PDF pp.97-100 | 25 Oct 2026 | No AFC approval implied.